


配置図 S=1:100

新昭和グループ 標準仕様 2×6 戸建住宅 参考設計図書
WITH EARTH / ウィザースホーム仕様 木造2階建 新築工事

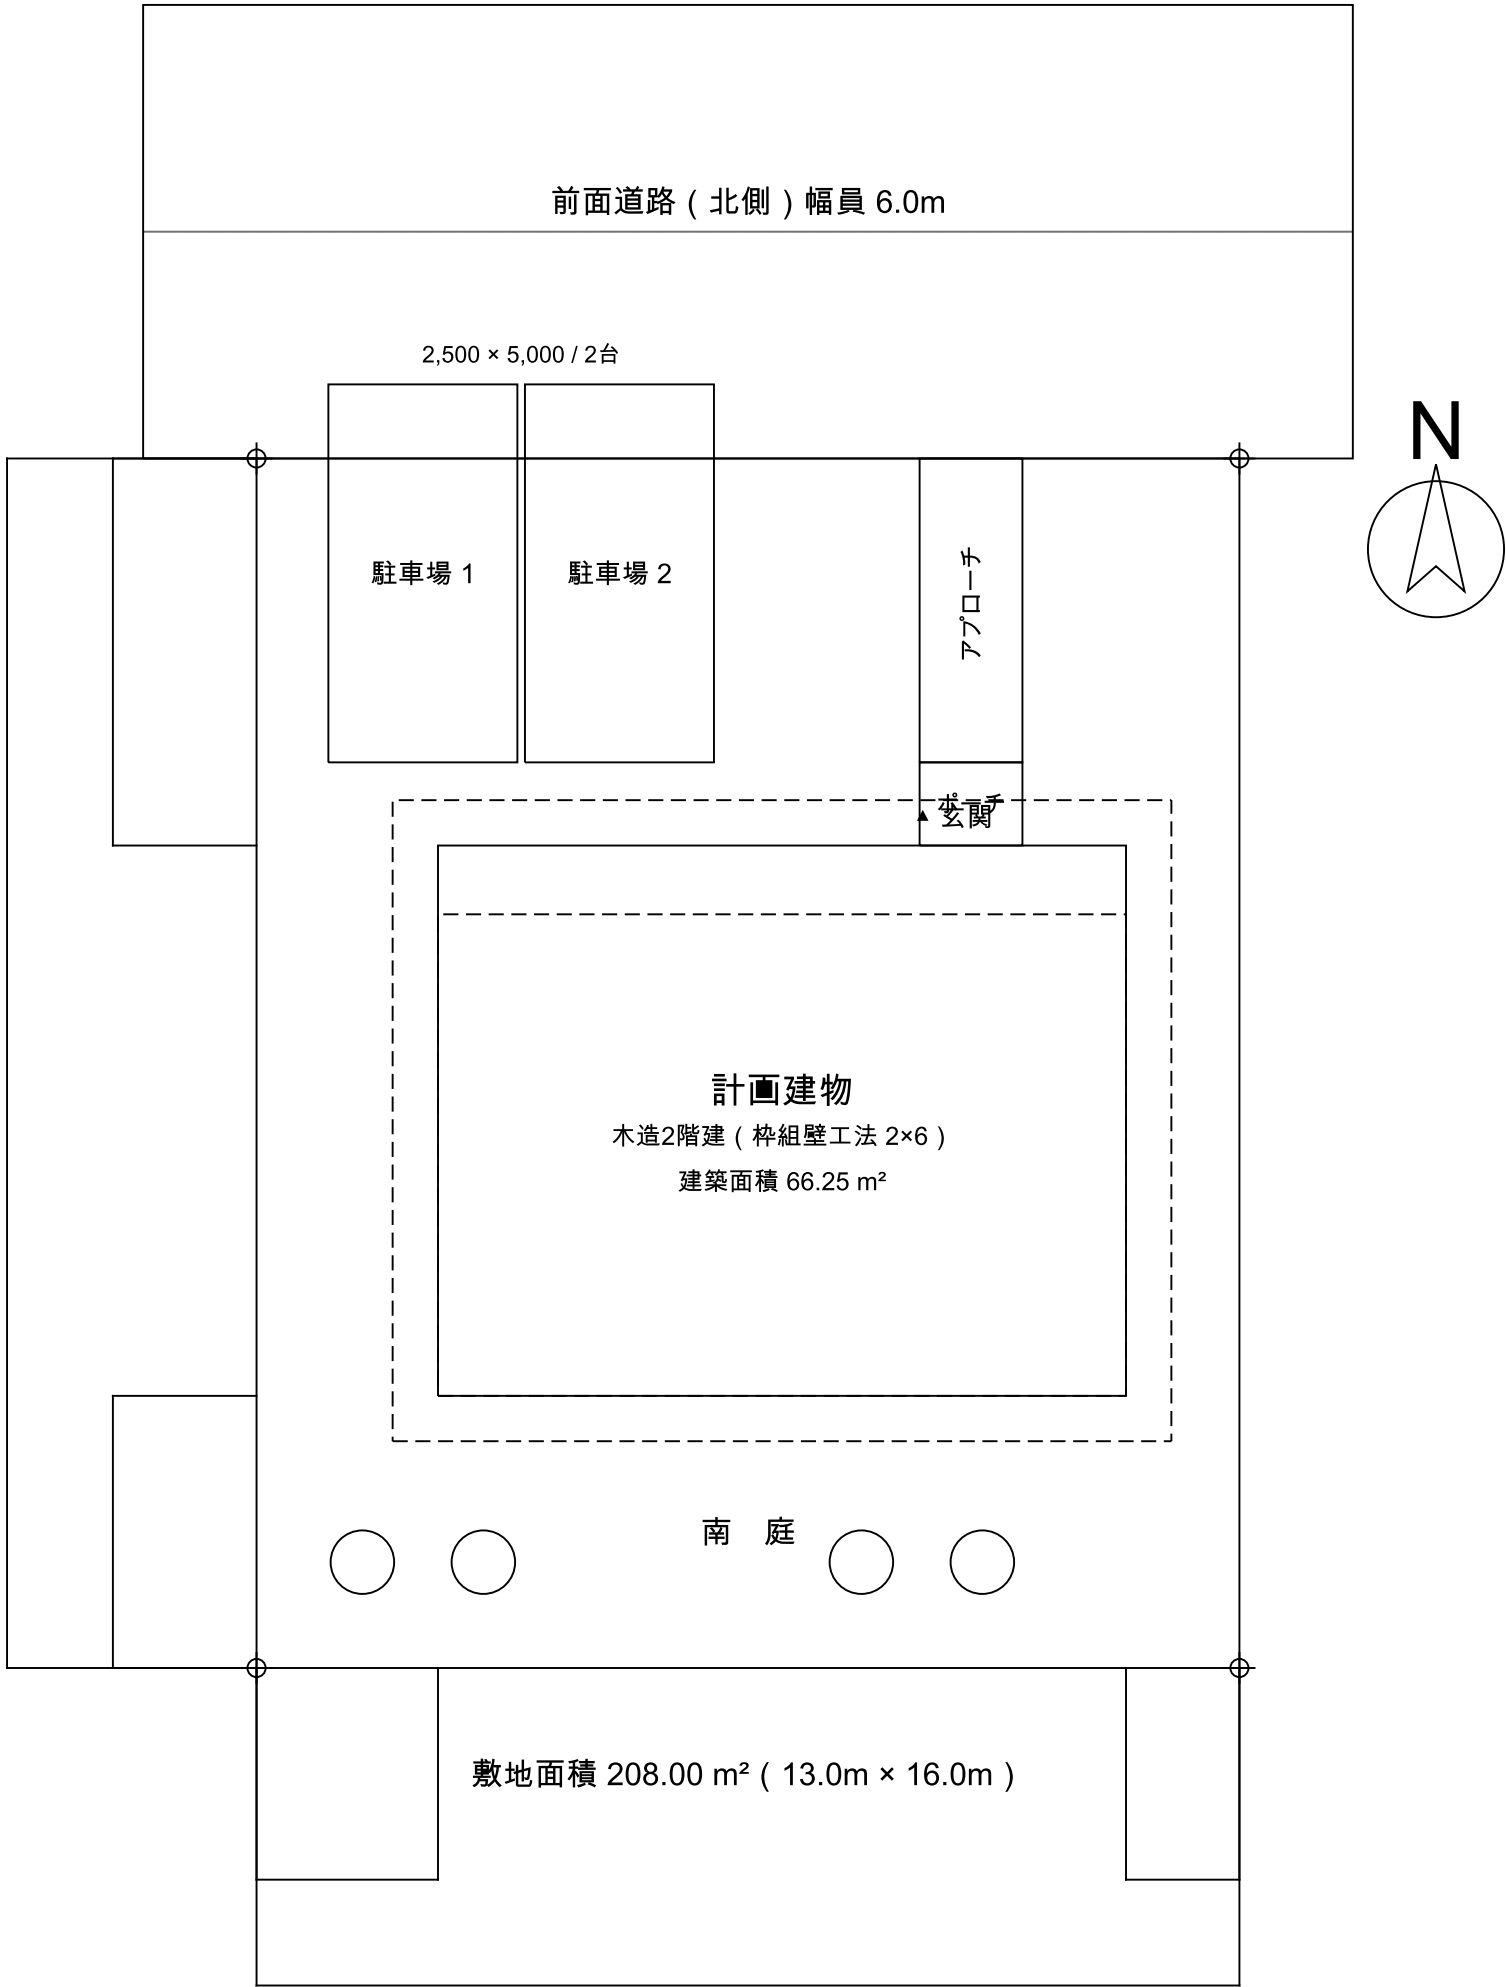

配 置 図 S=1:100

【敷地の条件】※ 設計条件として与えた値
用途地域 第一種低層住居専用地域
敷地面積 208.00 m²
前面道路 北側 幅員 6.0m
建蔽率 限度 50% 計画 31.85%
容積率 限度 100% 計画 59.72%
絶対高さ 限度 10m 計画 7.474m

【外構】
駐車場 2台 (2,500×5,000) を道路側に配置。
アプローチは玄関まで直線とし、段差を設けない。
南側に 3,600 の空地を確保し、LDK・和室の採光を確保する。

【ご確認をお願いしたい事項】
実案件では、用途地域・建蔽率 / 容積率・高さの限度・
道路幅員・敷地境界の確定測量結果を、都市計画情報および
確定測量図でご確認ください。これらは図面からは決まらず、
当方で数値を作ることはしていません。

【共通注記】
1. 寸法の単位は mm。特記なき限り通り芯 (壁芯) 寸法とする。
2. 構造は木造2階建 枠組壁工法 (2×6) とし、親会社 株式会社
新昭和「ウィザースホーム」の標準工法 (モノコック構造) に
準拠する。
3. 本図面集は参考プラン (架空案件) である。実在の敷地・施主
ではない。実施設計にあたっては敷地条件・地盤調査結果・
各種申請の指導事項を反映すること。
4. 法適合の検算結果は 03_計算書「法令適合検算書」を参照。
同書で『未検算』とした項目は合格ではない。

容積率 : 59.72 % / 限度 100 %
建蔽率 : 31.85 % / 限度 50 %
敷地面積 : 208.00 m²

配置図	
設計者	株式会社 Design RAVO
発注者	株式会社 新昭和 (親会社)
作成日	2026-09-14
縮 尺	S=1:100
図面番号	A-02