



2階平面図 S=1:50

新昭和グループ 標準仕様 2×6 戸建住宅 参考設計図書
WITH EARTH / ウィザースホーム仕様 木造2階建 新築工事

2階床面積 57.97 m² / 天井高 2,400 / 階高 2,800

【凡 例】
外壁 t200 (2×6 たて枠38×140 + 通気層 + 乾式外装タイル)
間仕切壁 t115 (2×4 たて枠38×89 + せっこうボード両面)
□ ... たて枠 (2×6) ーー ... 通り芯
AW/AD/BW/BD ... サッシ・玄関 SD/DR ... 室内建具
(仕様は A-08 建具表 を参照)

【注 記】
1. 寸法は通り芯 (壁芯) 寸法とする。単位 mm。
2. 室面積は壁芯で算定した数値であり、登記面積 (内法) とは一致しない。
3. 構造は木造2階建 枠組壁工法 (2×6) とし、親会社 株式会社新昭和「ウィザースホーム」の標準工法 (モノコック構造) に準拠する。
4. 本図は参考プラン (架空案件) である。実施設計にあたっては敷地条件・地盤調査結果・各種申請の指導事項を反映すること。

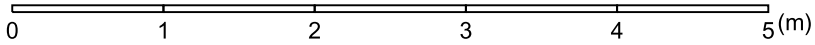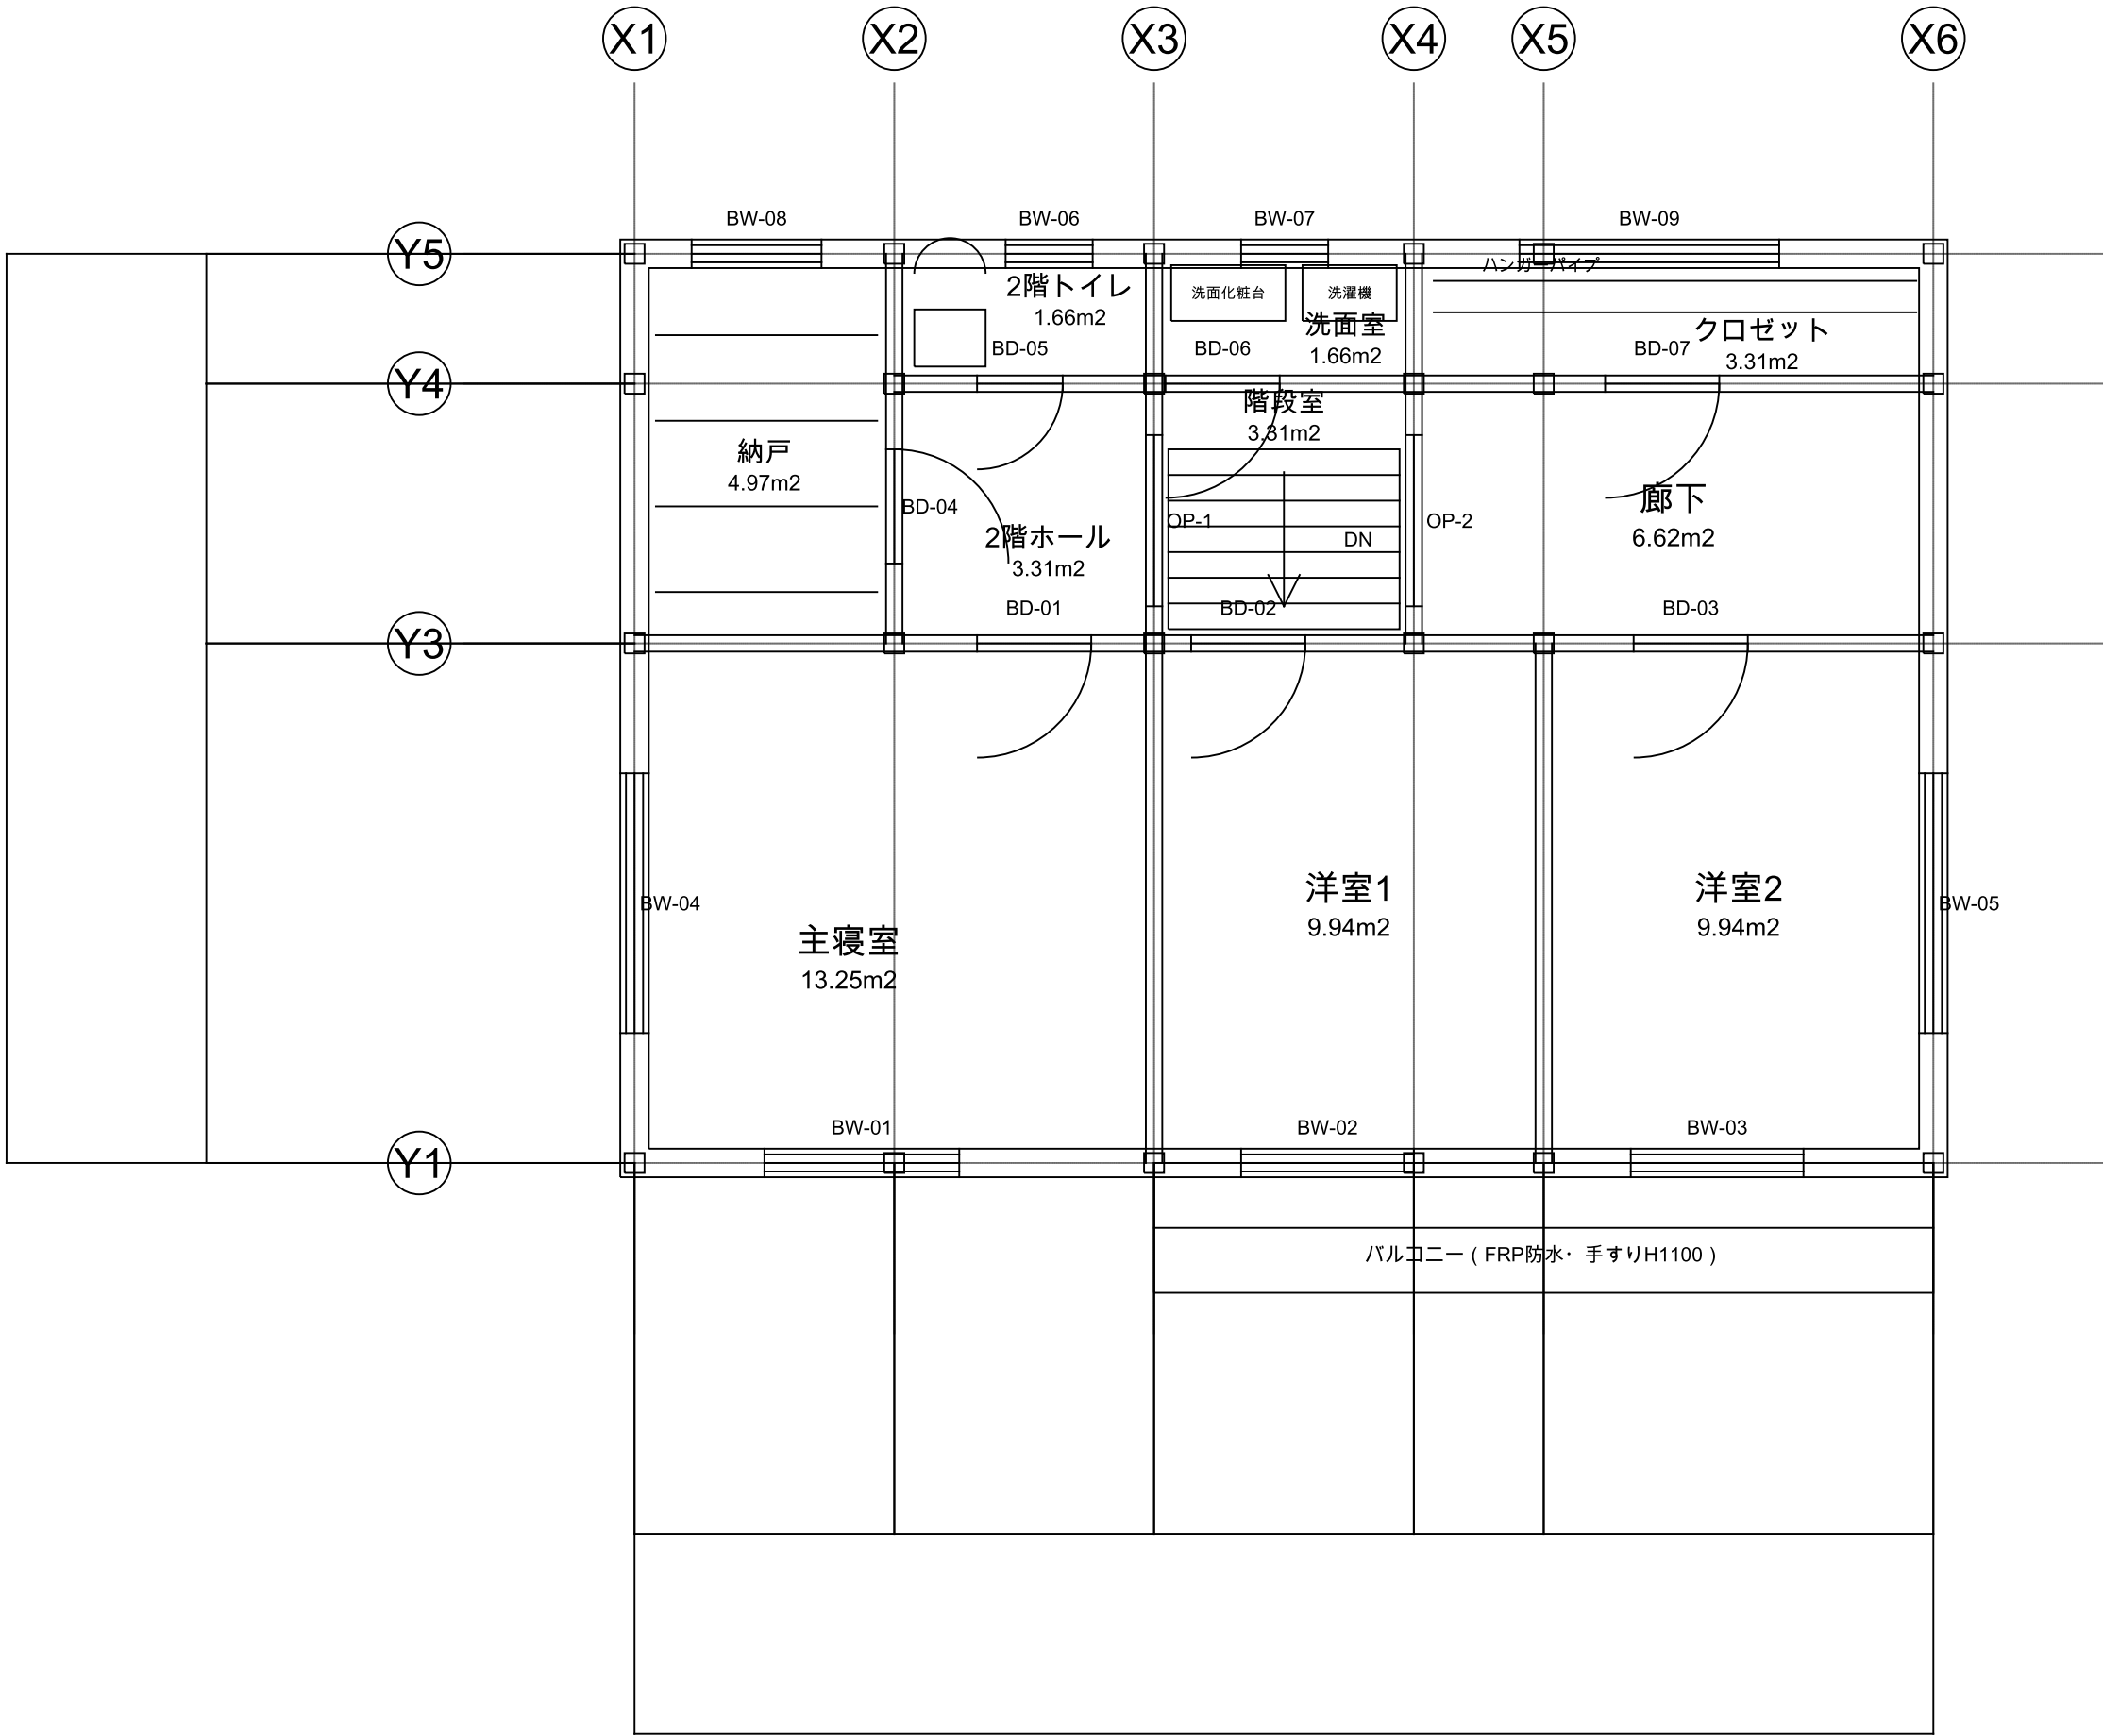

構造 : 木造 枠組壁工法 (2×6)
床面積 : 57.97 m²

2階平面図	
設計者	株式会社 Design RAVO
発注者	株式会社 新昭和 (親会社)
作成日	2026-09-14
縮 尺	S=1:50
図面番号	A-04