
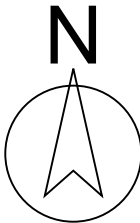


屋根伏図 S=1:50

新昭和グループ 標準仕様 2×6 戸建住宅 参考設計図書
WITH EARTH / ウィザースホーム仕様 木造2階建 新築工事

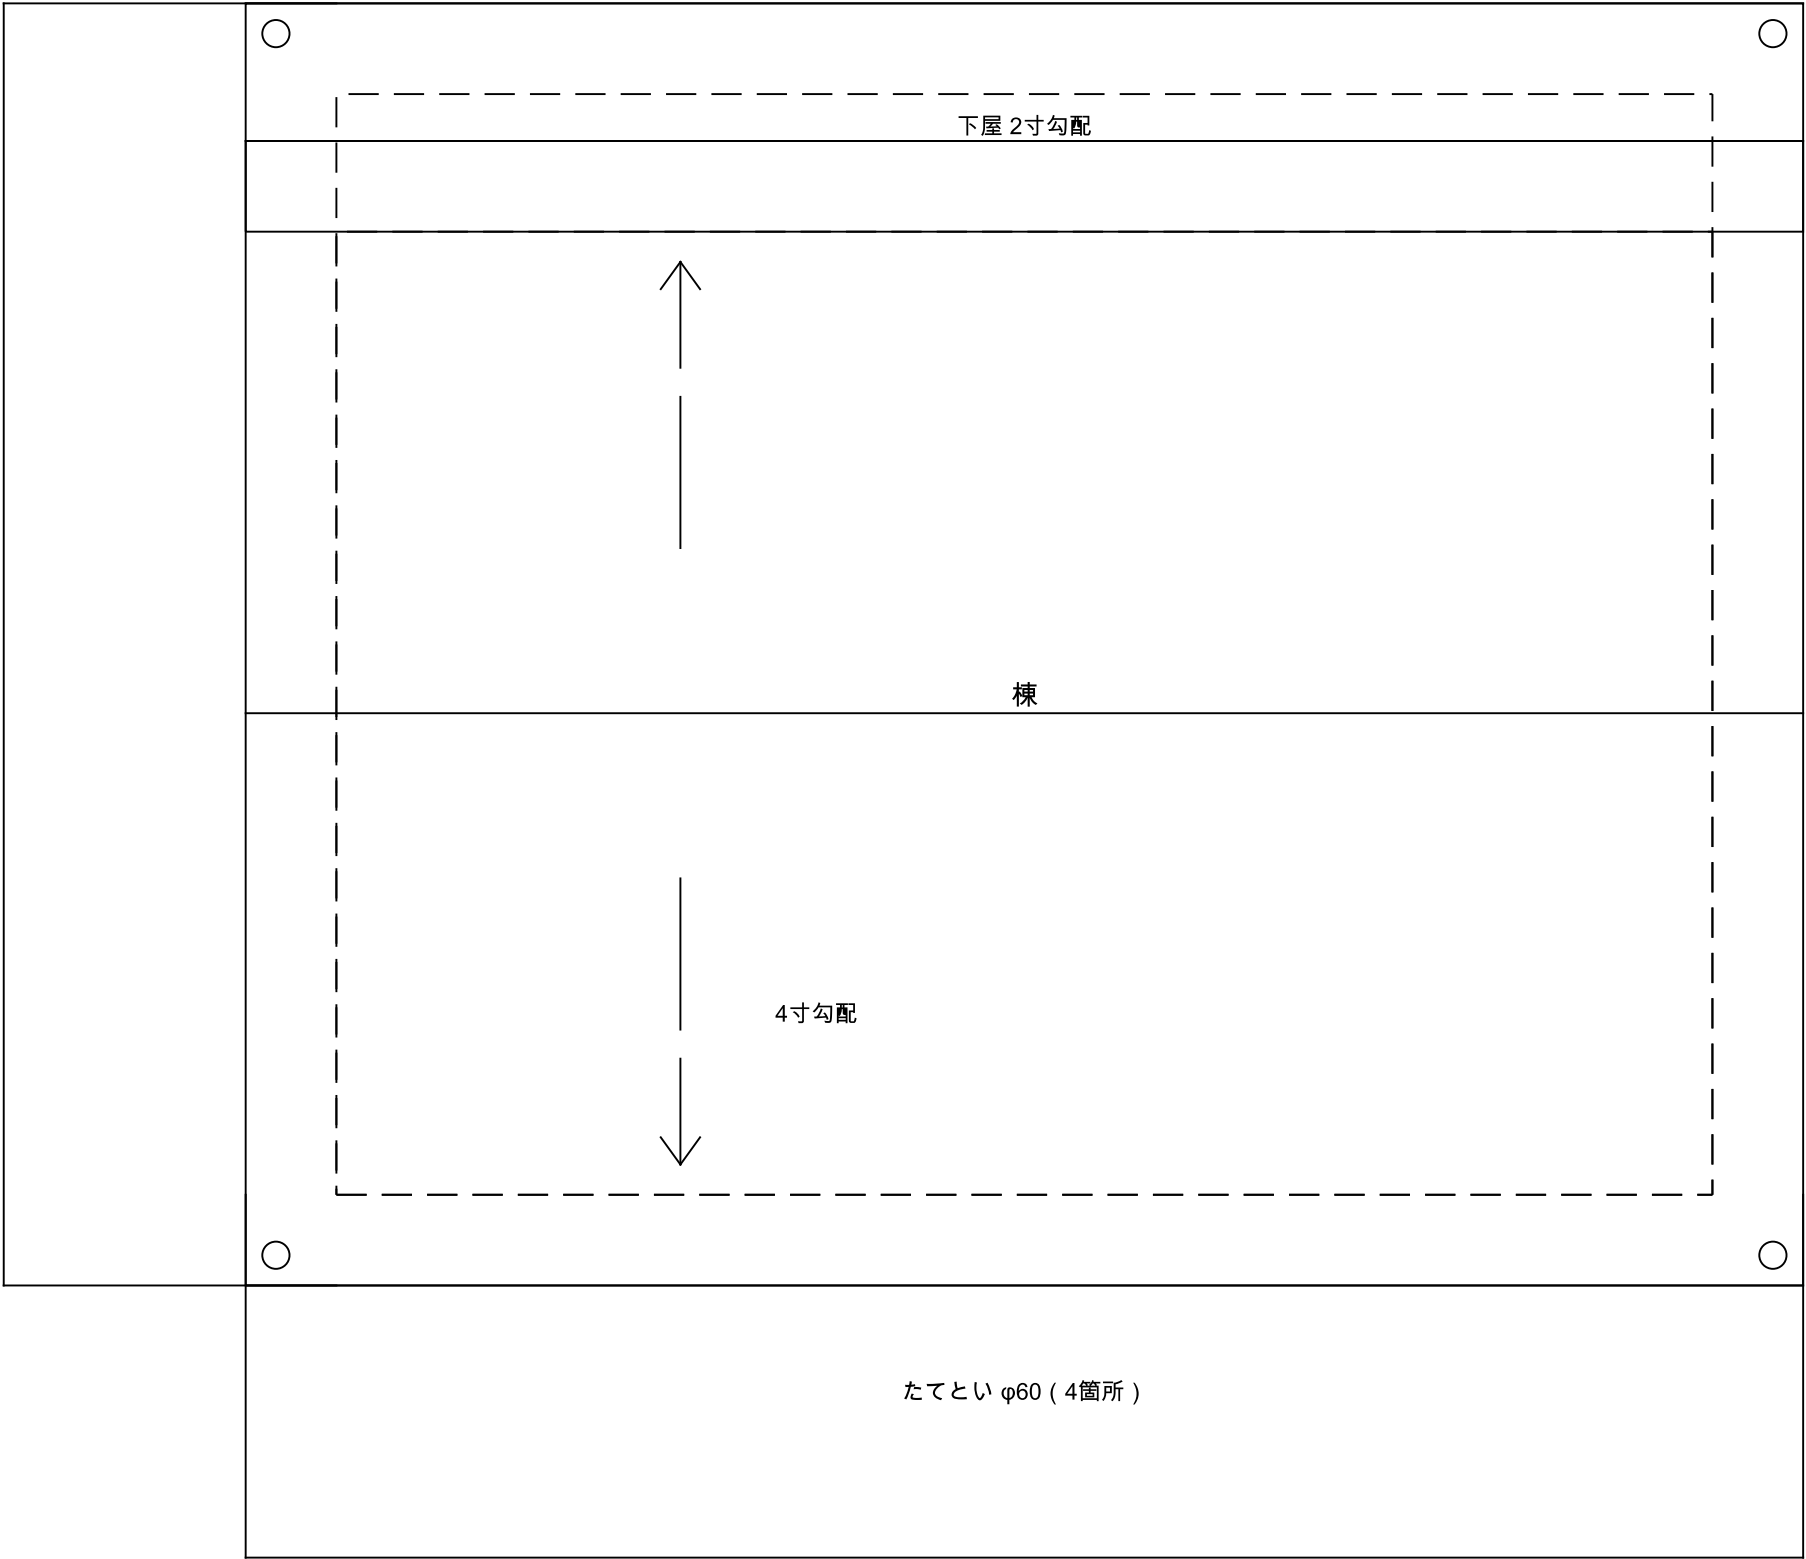

【屋根仕様】
ガルバリウム鋼板 t0.35 立平葺
改質アスファルトルーフィング / 構造用合板 t12
主屋根 4寸勾配 (切妻・棟は東西方向)
下屋 2寸勾配 (北側 1階張り出し部)
軒の出・ けらば出とも 600

【とい】
軒どい 半丸105 / たてとい φ60 (4箇所)

【換気】
軒天換気材を軒裏全長に設ける。
小屋裏換気は天井面積の 1/250 以上を確保すること
(実面積の確定は実施設計時)。

【共通注記】
1. 寸法の単位は mm。特記なき限り通り芯 (壁芯) 寸法とする。
2. 構造は木造2階建 枠組壁工法 (2×6) とし、親会社 株式会社
新昭和「ウィザースホーム」の標準工法 (モノコック構造) に
準拠する。
3. 本図面集は参考プラン (架空案件) である。実在の敷地・ 施主
ではない。実施設計にあたっては敷地条件・ 地盤調査結果・
各種申請の指導事項を反映すること。
4. 法適合の検算結果は 03_計算書「法令適合検算書」を参照。
同書で『未検算』とした項目は合格ではない。

屋 根 伏 図 S=1:50

軒の出 : 600
屋根勾配 : 主屋根 4寸 / 下屋 2寸

屋根伏図	
設計者	株式会社 Design RAVO
発注者	株式会社 新昭和 (親会社)
作成日	2026-09-14
縮 尺	S=1:50
図面番号	A-07