


基礎伏図 S=1:50

新昭和グループ 標準仕様 2×6 戸建住宅 参考設計図書
WITH EARTH / ウィザースホーム仕様 木造2階建 新築工事

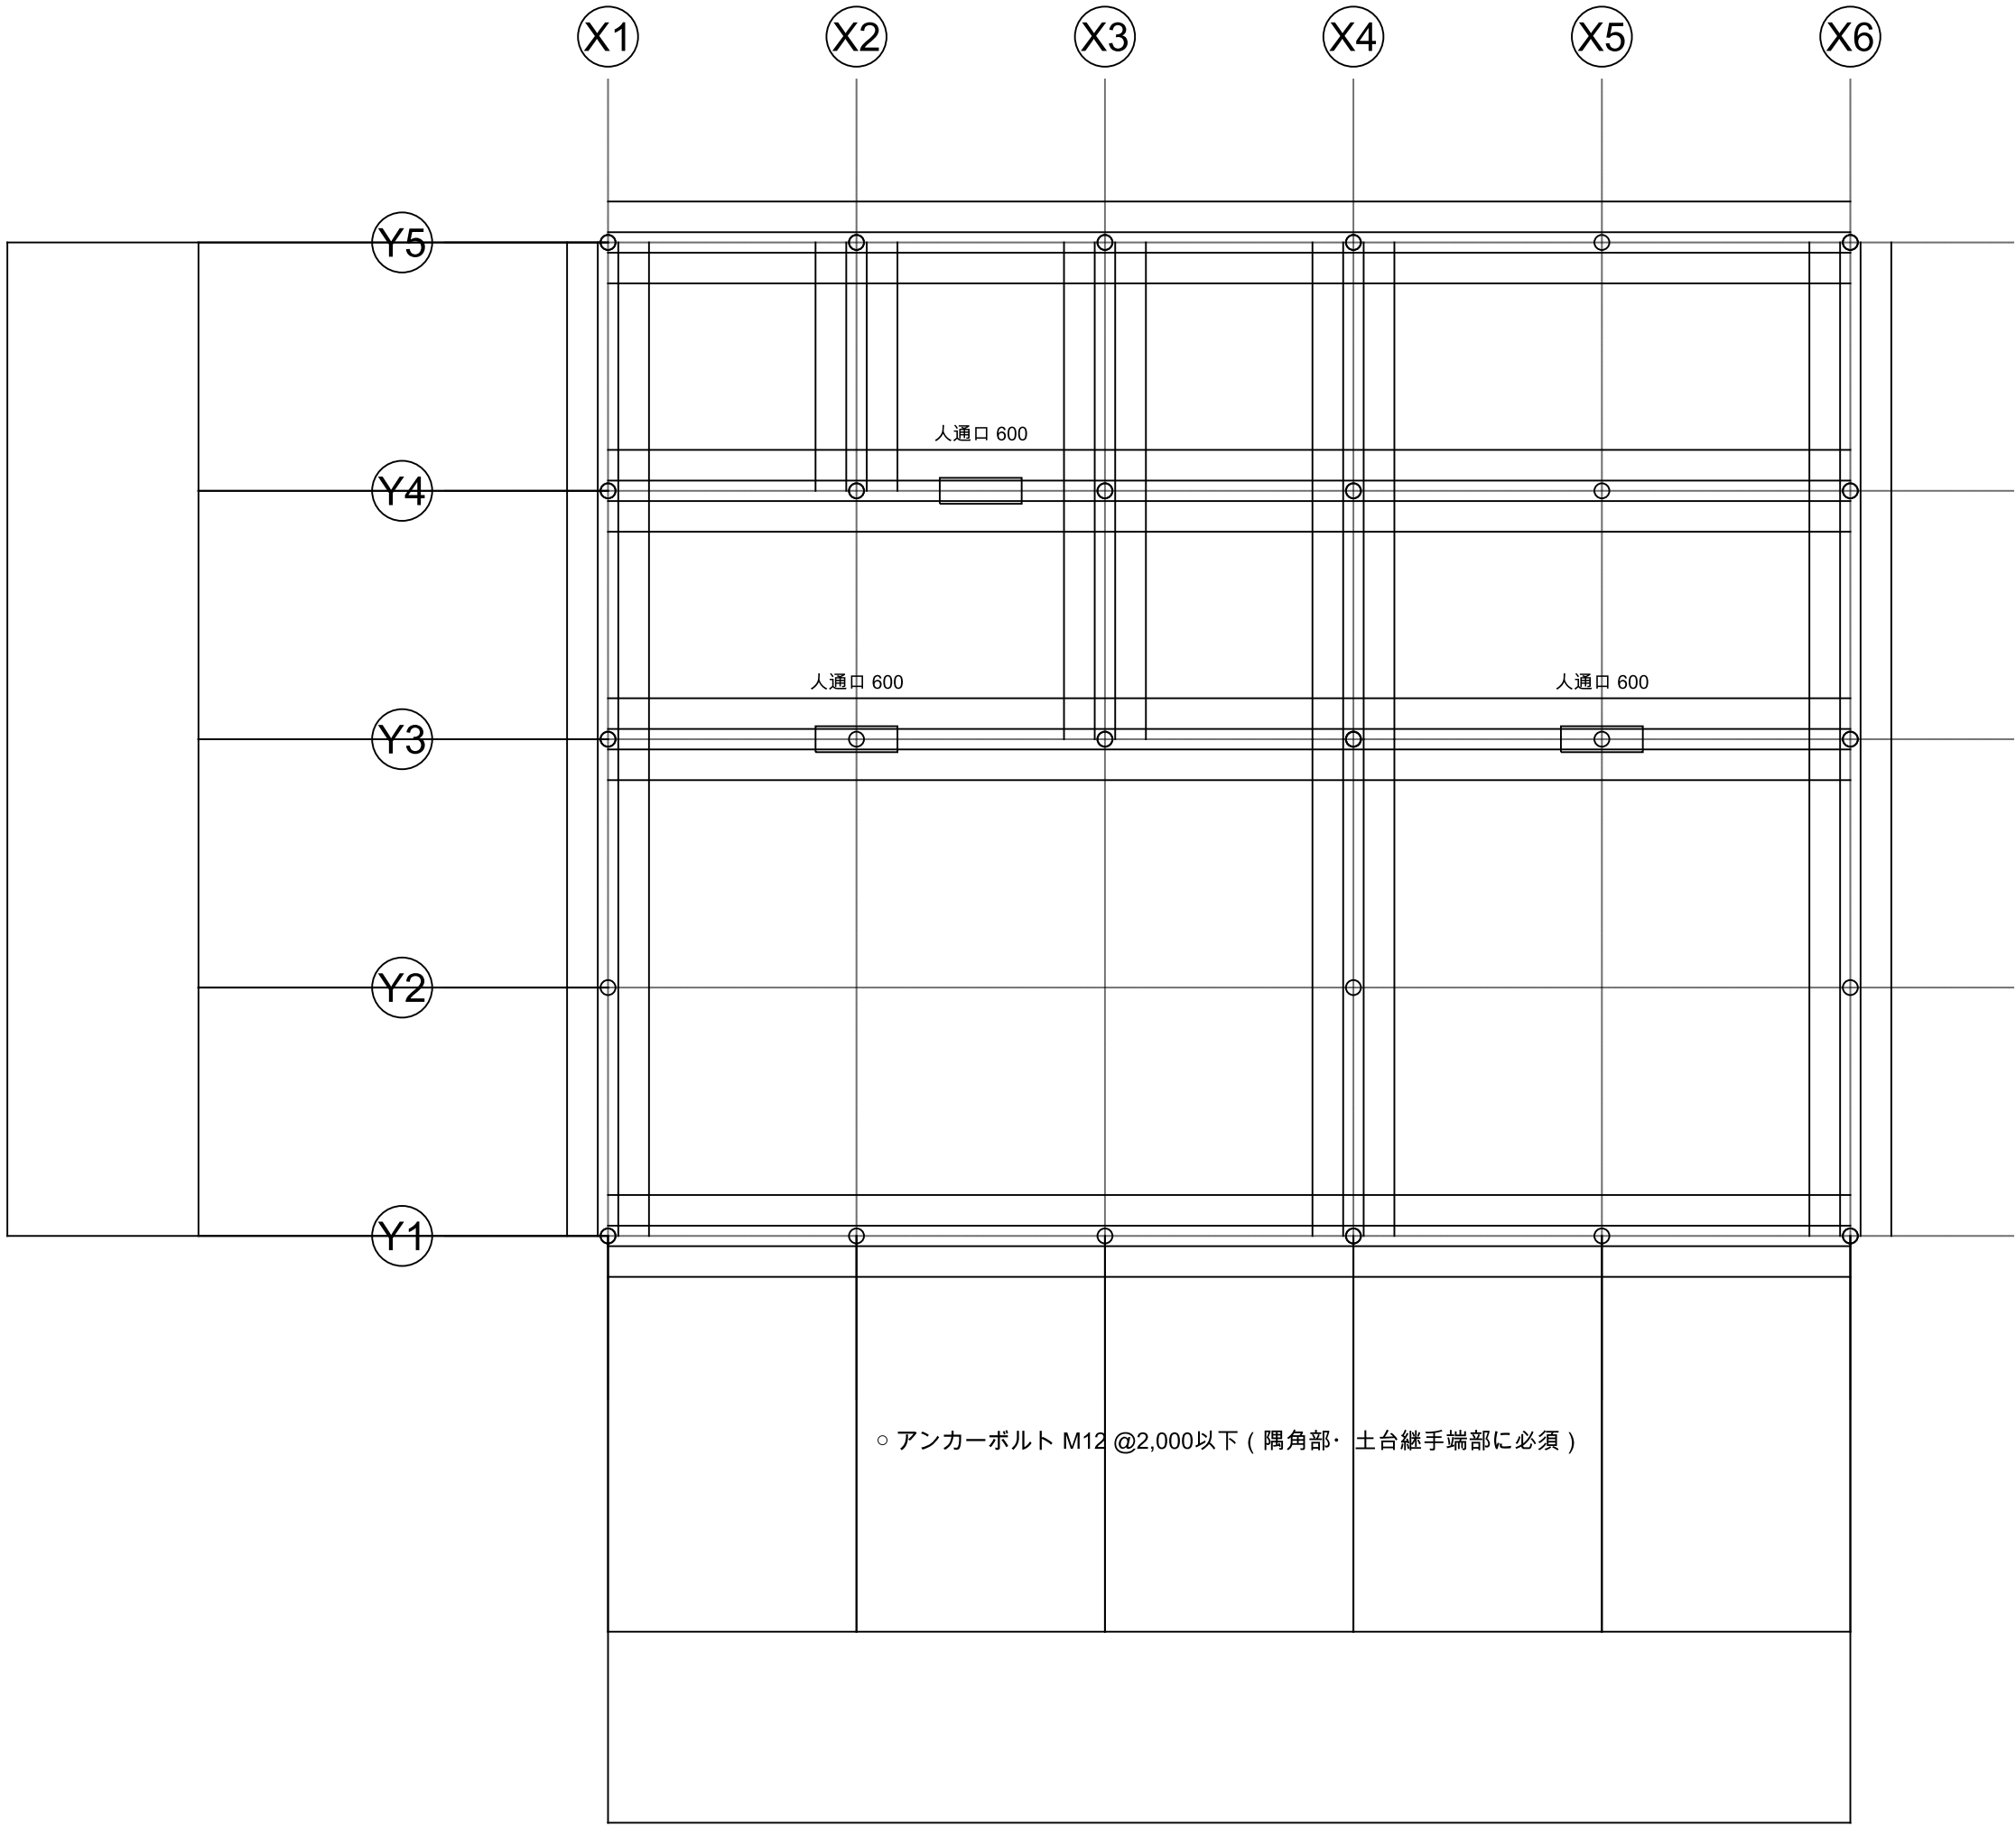

【基礎仕様】
形式 鉄筋コンクリート造 布基礎 (底盤: 立上り一体打ち)
立上り t150 × H450 (GL+400 / FL-100)
フーチング W600 × t150
配筋 立上り 主筋 D13 上下各1本 / 補強筋 D10 @300
底盤 D13 @200 シングル
かぶり 土に接する部分 60mm 以上
土間 防湿コンクリート t60 / 防湿フィルム t0.15
アンカーボルト M12 @2,000 以下
(隅角部・土台継手端部には必ず設ける)

【ご用意いただくもの】
地盤調査報告書 (許容応力度)。基礎が地盤に支えられるかの検定は、この値が無いと行えません。当方では作りません。

【共通注記】
1. 寸法の単位は mm。特記なき限り通り芯 (壁芯) 寸法とする。
2. 構造は木造2階建 枠組壁工法 (2×6) とし、親会社 株式会社新昭和「ウィザースホーム」の標準工法 (モノコック構造) に準拠する。
3. 本図面集は参考プラン (架空案件) である。実在の敷地・施主ではない。実施設計にあたっては敷地条件・地盤調査結果・各種申請の指導事項を反映すること。
4. 法適合の検算結果は 03_計算書「法令適合検算書」を参照。同書で『未検算』とした項目は合格ではない。

立上り : t150 × H450
基礎形式 : 布基礎 (一体打ち)

基礎伏図	
設計者	株式会社 Design RAVO
発注者	株式会社 新昭和 (親会社)
作成日	2026-09-14
縮 尺	S=1:50
図面番号	S-01

基 礎 伏 図 S=1:50