

新昭和グループ 標準仕様 2×6 戸建住宅

参 考 設 計 図 書

WITH EARTH / ウィザースホーム仕様 木造2階建 新築工事

■ 建 築 概 要

項 目	内 容
工 事 名 称	新昭和グループ 標準仕様 2×6 戸建住宅 参考設計図書
建 物 用 途	一戸建ての住宅
構 造 ・ 規 模	木造2階建 枠組壁工法 (2×6) モノコック構造
敷 地 面 積	208.00 m²
建 築 面 積	66.25 m² (建蔽率 31.85% / 限度 50%)
延 べ 面 積	124.22 m² (容積率 59.72% / 限度 100%)
1 階 床 面 積	66.25 m²
2 階 床 面 積	57.97 m²
最 高 の 高 さ	GL + 7,474 (7.474 m)
軒 の 高 さ	GL + 6,200 (6.200 m)
階 高 ・ 天 井 高	1階 2,900 / 2階 2,800 天井高 2,400
用 途 地 域	第一種低層住居専用地域 (設計条件)
屋 根 ・ 外 壁	ガルバリウム鋼板 立平葺 (4寸勾配) / 乾式外装タイル 45二丁
基 礎	鉄筋コンクリート造 布基礎 (立上り t150 H450)
設 計 者	株式会社 Design RAVO (沖縄県那覇市字小禄1831-1 沖縄産業支援センター701)
発 注 者	株式会社 新昭和 (親会社)
備 考	参考プラン (架空案件) 。実在の敷地・ 施主ではない。

■ 図 面 リ ス ト (意匠図・ 構造図)

図面番号	図 面 名 称	縮 尺
A-00	表紙・ 建築概要・ 図面リスト	—
A-01	面積求積図・ 面積表	1:100
A-02	配置図	1:100
A-03	1階平面図	1:50
A-04	2階平面図	1:50
A-05	立面図 (南・ 東・ 北・ 西)	1:100
A-06	断面図 (A-A'・ B-B')	1:100
A-07	屋根伏図	1:50
A-08	建具表	—
A-09	仕上表	—
S-01	基礎伏図	1:50
S-02	床伏図 (1階・ 2階)	1:100
S-03	小屋伏図	1:50
S-04	耐力壁配置図 (1階・ 2階)	1:100

■ 計 算 書 ・ 報 告 書

番号	計 算 書 ・ 報 告 書 名 称
計-01	設計条件書
計-02	構造計算書 (壁量・ 四分割法・ 偏心率・ 地震力)
計-03	法令適合検算書 (1階・ 2階)
計-04	ご用意いただくもの・ 未検算項目一覧

【この図面集について】

株式会社 Design RAVO が日常的に作成している建築設計図書
(意匠設計・ 構造設計・ 各種申請) の構成に合わせた参考図面集です。
親会社 株式会社新昭和の住宅ブランド「ウィザースホーム」の
標準工法である 2×6 (ツーバイシックス) 枠組壁工法・ モノコック
構造を前提としています。

【図面と計算書の関係】

面積・ 壁量・ 耐力壁の位置は、平面図の通り芯寸法から機械で
計算した値をそのまま用いています。図面の寸法を書き換えると
計算書の数値も同時に変わるため、図と数値が食い違いません。

【未検算の扱い】

法令検算・ 構造計算のうち、所在地・ 地盤調査・ 材料の等級が
決まって初めて算定できる項目は『未検算』として開示しています。
未検算は合格ではありません。詳細は 計-04 をご覧ください。

【共通注記】

- 寸法の単位は mm。特記なき限り通り芯 (壁芯) 寸法とする。
- 構造は木造2階建 枠組壁工法 (2×6) とし、親会社 株式会社
新昭和「ウィザースホーム」の標準工法 (モノコック構造) に
準拠する。
- 本図面集は参考プラン (架空案件) である。実在の敷地・ 施主
ではない。実施設計にあたっては敷地条件・ 地盤調査結果・
各種申請の指導事項を反映すること。
- 法適合の検算結果は 03_計算書「法令適合検算書」を参照。
同書で『未検算』とした項目は合格ではない。


構造：木造2階建 枠組壁工法 (2×6)

延べ面積：124.22 m²

表紙・ 建築概要・ 図面リスト	
設計者	株式会社 Design RAVO
発注者	株式会社 新昭和 (親会社)
作成日	2026-09-14
縮 尺	S=1:50
図面番号	A-00

面積求積図・ 面積表 S=1:100

新昭和グループ 標準仕様 2×6 戸建住宅 参考設計図書
WITH EARTH / ウィザースホーム仕様 木造2階建 新築工事

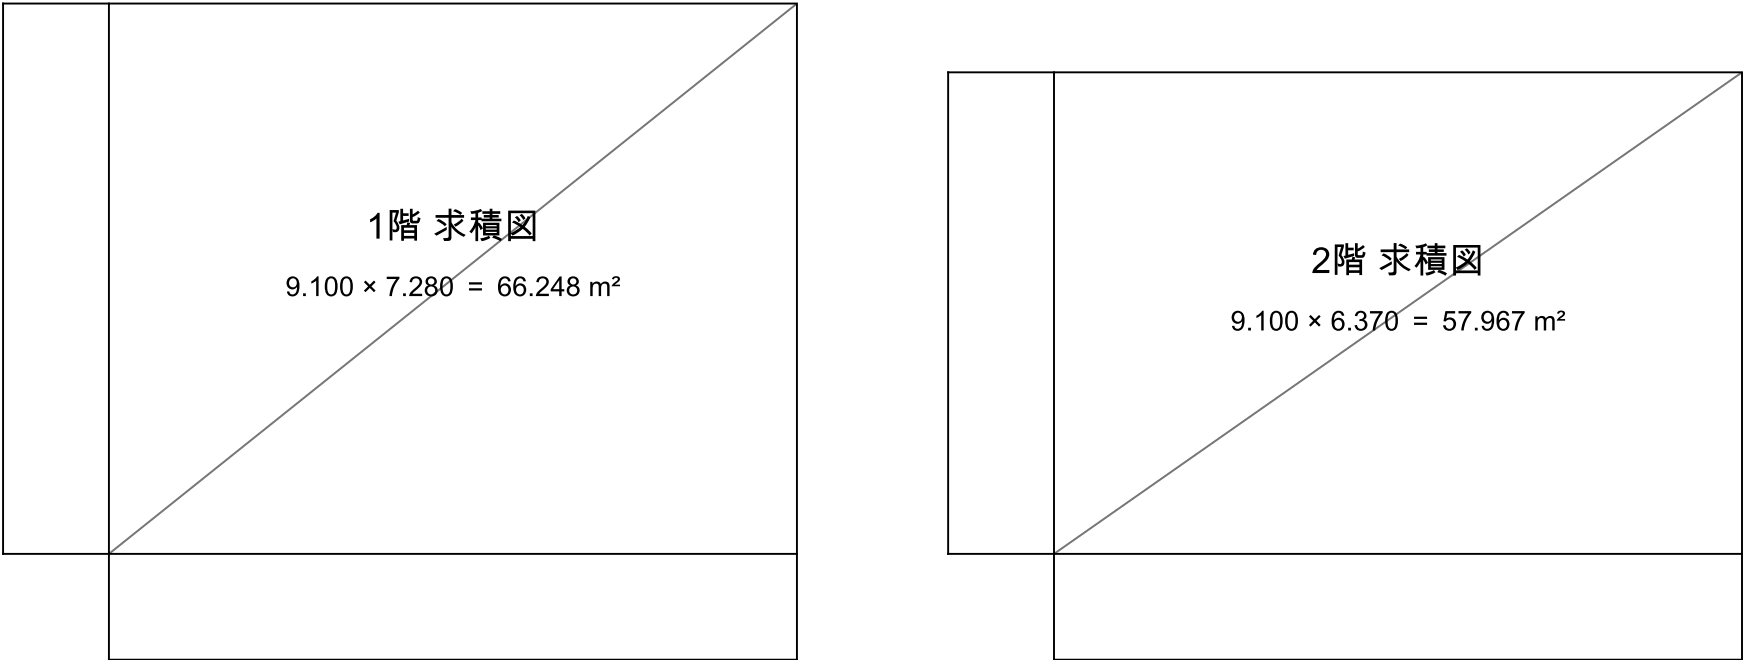

S=1:100

S=1:100

■ 面 積 表

区 分	算 式 (m)	面 積 (m²)	備 考
1階	9.100 × 7.280	66.248	壁芯
2階	9.100 × 6.370	57.967	壁芯
延べ面積	—	124.215	1階 + 2階
建築面積	9.100 × 7.280	66.248	バルコニーの出 910 (1m未満) は不算入
敷地面積	13.0 × 16.0	208.000	設計条件

■ 建蔽率・容積率・高さ (設計条件に基づく算定)

項 目	算 式	値	限 度・根拠
建蔽率	66.25 ÷ 208.00	31.85 %	限度 50 % (第一種低層住居専用地域)
容積率	124.22 ÷ 208.00	59.72 %	限度 100 % (同上)
最高の高さ	—	7.474 m	絶対高さの限度 10 m

※ 用途地域・ 建蔽率 / 容積率の限度・ 絶対高さの限度は設計条件として与えた値である。実案件では都市計画情報で必ず確認すること。

【面積の考え方】

- ・ 各階の面積は壁芯 (通り芯) で算定する。
- ・ 登記面積 (内法) とは一致しない。
- ・ バルコニーは外壁面からの出が 910 (1m未満) のため、
建築面積・ 床面積とも不算入とした。

【この表の数値の出どころ】

平面図の通り芯寸法から機械で計算した値をそのまま印字している。図面の寸法を書き換えれば、この表の数値も同時に変わる (手で書き写していない) 。

【共通注記】


1. 寸法の単位は mm。特記なき限り通り芯 (壁芯) 寸法とする。
2. 構造は木造2階建 枠組壁工法 (2×6) とし、親会社 株式会社 新昭和「ウィザースホーム」の標準工法 (モノコック構造) に準拠する。
3. 本図面集は参考プラン (架空案件) である。実在の敷地・ 施主ではない。実施設計にあたっては敷地条件・ 地盤調査結果・ 各種申請の指導事項を反映すること。
4. 法適合の検算結果は 03_計算書「法令適合検算書」を参照。
同書で『未検算』とした項目は合格ではない。

建築面積 : 66.25 m²
延べ面積 : 124.22 m²

面積求積図・ 面積表	
設計者	株式会社 Design RAVO
発注者	株式会社 新昭和 (親会社)
作成日	2026-09-14
縮 尺	S=1:100
図面番号	A-01

配置図 S=1:100

新昭和グループ 標準仕様 2×6 戸建住宅 参考設計図書
WITH EARTH / ウィザースホーム仕様 木造2階建 新築工事

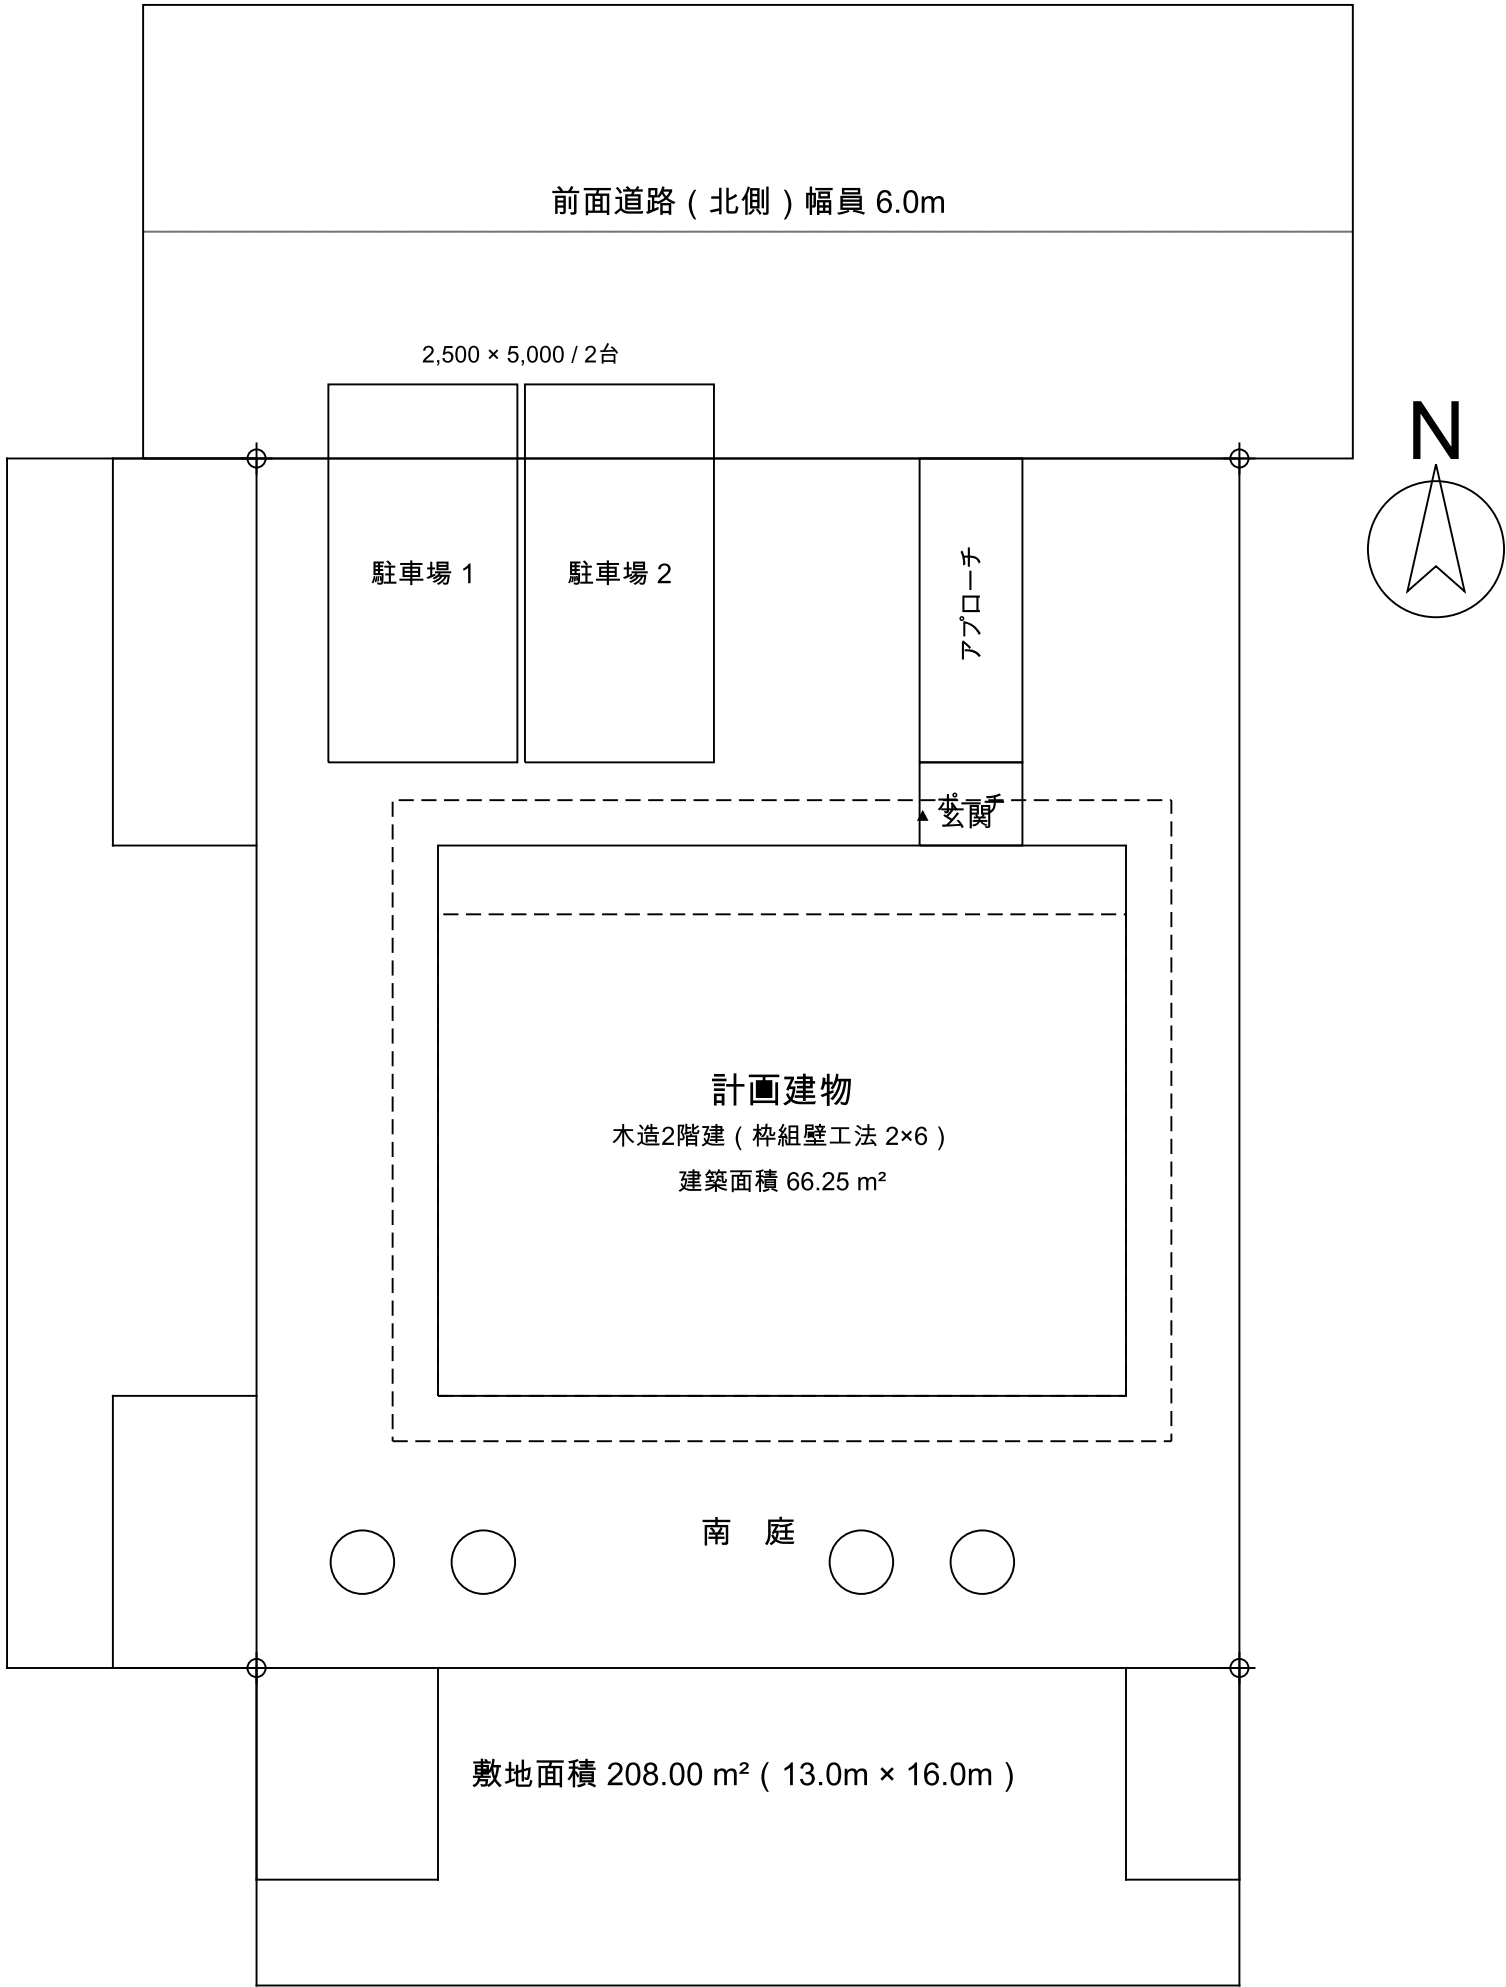

配置図 S=1:100

【敷地の条件】※ 設計条件として与えた値
用途地域 第一種低層住居専用地域
敷地面積 208.00 m²
前面道路 北側 幅員 6.0m
建蔽率 限度 50% 計画 31.85%
容積率 限度 100% 計画 59.72%
絶対高さ 限度 10m 計画 7.474m

【外構】
駐車場 2台 (2,500×5,000) を道路側に配置。
アプローチは玄関まで直線とし、段差を設けない。
南側に 3,600 の空地を確保し、LDK・和室の採光を確保する。

【ご確認をお願いしたい事項】
実案件では、用途地域・建蔽率 / 容積率・高さの限度・
道路幅員・敷地境界の確定測量結果を、都市計画情報および
確定測量図でご確認ください。これらは図面からは決まらず、
当方で数値を作ることはしていません。

【共通注記】
1. 寸法の単位は mm。特記なき限り通り芯 (壁芯) 寸法とする。
2. 構造は木造2階建 枠組壁工法 (2×6) とし、親会社 株式会社
新昭和「ウィザースホーム」の標準工法 (モノコック構造) に
準拠する。
3. 本図面集は参考プラン (架空案件) である。実在の敷地・施主
ではない。実施設計にあたっては敷地条件・地盤調査結果・
各種申請の指導事項を反映すること。
4. 法適合の検算結果は 03_計算書「法令適合検算書」を参照。
同書で『未検算』とした項目は合格ではない。

容積率 : 59.72 % / 限度 100 %
建蔽率 : 31.85 % / 限度 50 %
敷地面積 : 208.00 m²

配置図	
設計者	株式会社 Design RAVO
発注者	株式会社 新昭和 (親会社)
作成日	2026-09-14
縮 尺	S=1:100
図面番号	A-02



1階平面図 S=1:50

新昭和グループ 標準仕様 2×6 戸建住宅 参考設計図書
WITH EARTH / ウィザースホーム仕様 木造2階建 新築工事

1階床面積 66.25 m² / 天井高 2,400 / 階高 2,900

【凡 例】
外壁 t200 (2×6 たて枠38×140 + 通気層 + 乾式外装タイル)
間仕切壁 t115 (2×4 たて枠38×89 + セッコウボード両面)
□ ... たて枠 (2×6) ーー ... 通り芯
AW/AD/BW/BD ... サッシ・玄関 SD/DR ... 室内建具
(仕様は A-08 建具表 を参照)

【注 記】
1. 寸法は通り芯 (壁芯) 寸法とする。単位 mm。
2. 室面積は壁芯で算定した数値であり、登記面積 (内法) とは一致しない。
3. 構造は木造2階建 枠組壁工法 (2×6) とし、親会社 株式会社新昭和「ウィザースホーム」の標準工法 (モノコック構造) に準拠する。
4. 本図は参考プラン (架空案件) である。実施設計にあたっては敷地条件・地盤調査結果・各種申請の指導事項を反映すること。

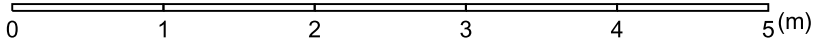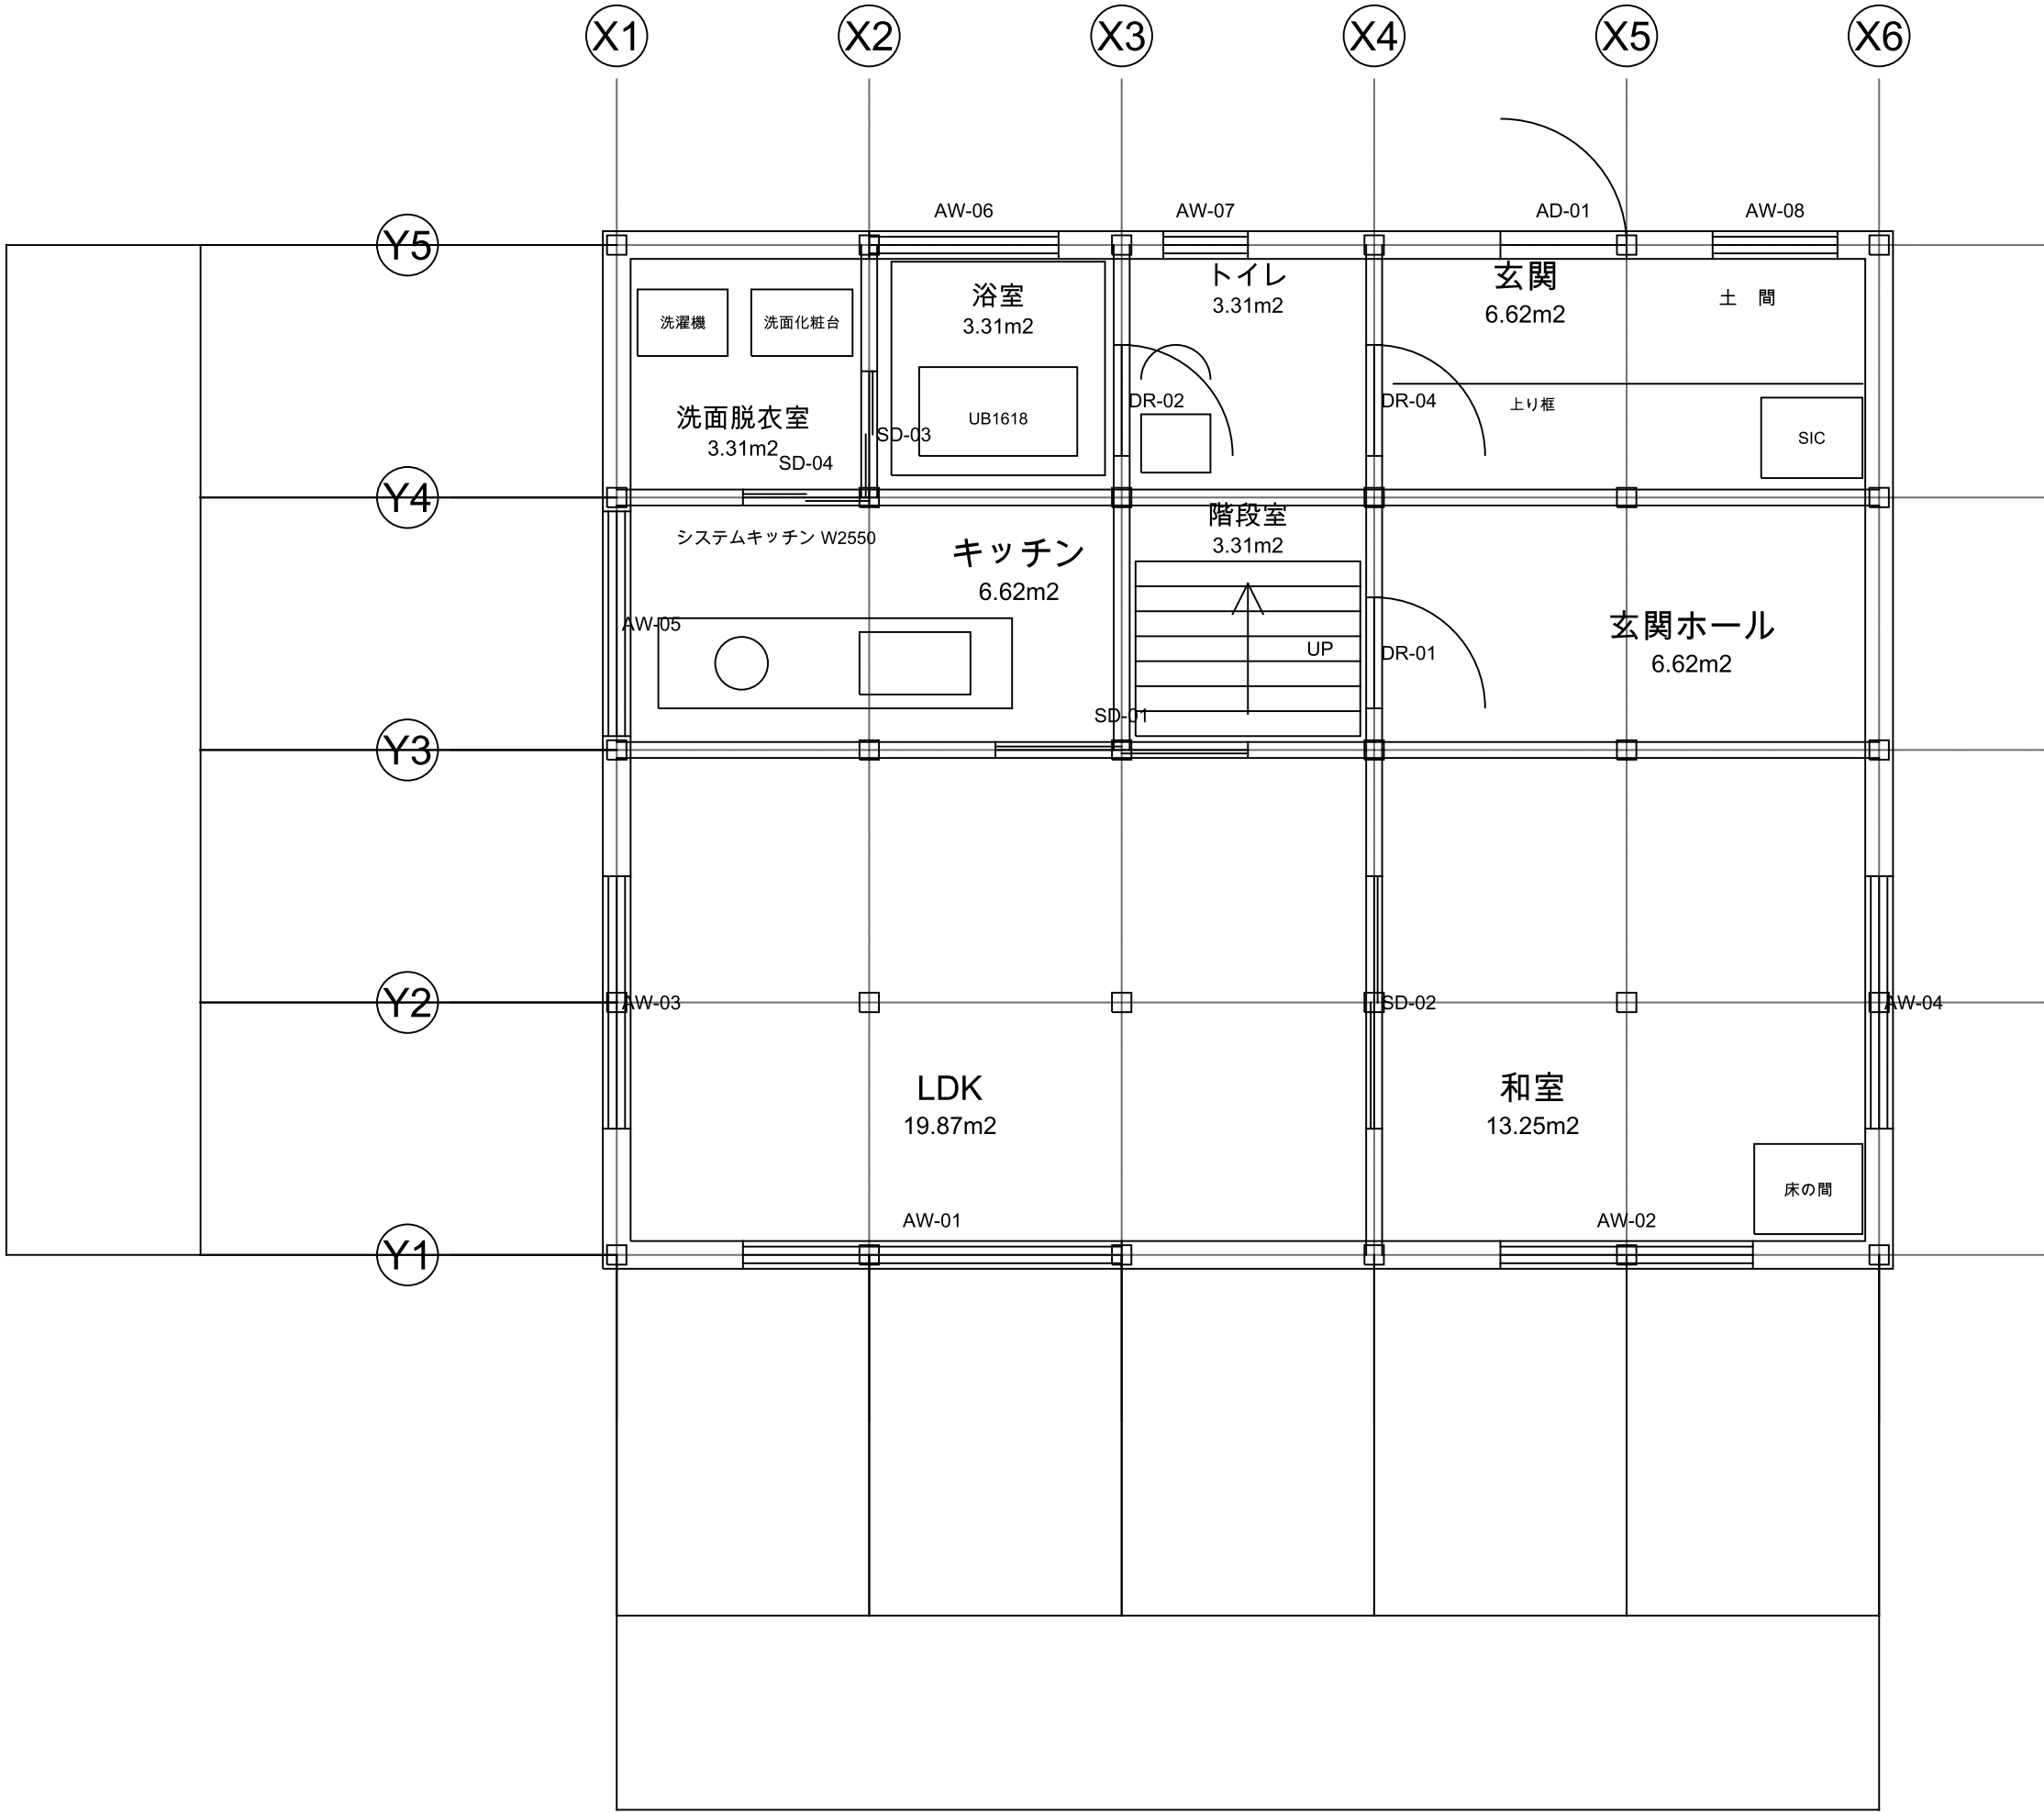

構造 : 木造 枠組壁工法 (2×6)
床面積 : 66.25 m²

1階平面図	
設計者	株式会社 Design RAVO
発注者	株式会社 新昭和 (親会社)
作成日	2026-09-14
縮 尺	S=1:50
図面番号	A-03


2階平面図 S=1:50

新昭和グループ 標準仕様 2×6 戸建住宅 参考設計図書
WITH EARTH / ウィザースホーム仕様 木造2階建 新築工事

2階床面積 57.97 m² / 天井高 2,400 / 階高 2,800

【凡 例】
外壁 t200 (2×6 たて枠38×140 + 通気層 + 乾式外装タイル)
間仕切壁 t115 (2×4 たて枠38×89 + せっこうボード両面)
□ ... たて枠 (2×6) ーー ... 通り芯
AW/AD/BW/BD ... サッシ・玄関 SD/DR ... 室内建具
(仕様は A-08 建具表 を参照)

【注 記】
1. 寸法は通り芯 (壁芯) 寸法とする。単位 mm。
2. 室面積は壁芯で算定した数値であり、登記面積 (内法) とは一致しない。
3. 構造は木造2階建 枠組壁工法 (2×6) とし、親会社 株式会社新昭和「ウィザースホーム」の標準工法 (モノコック構造) に準拠する。
4. 本図は参考プラン (架空案件) である。実施設計にあたっては敷地条件・地盤調査結果・各種申請の指導事項を反映すること。

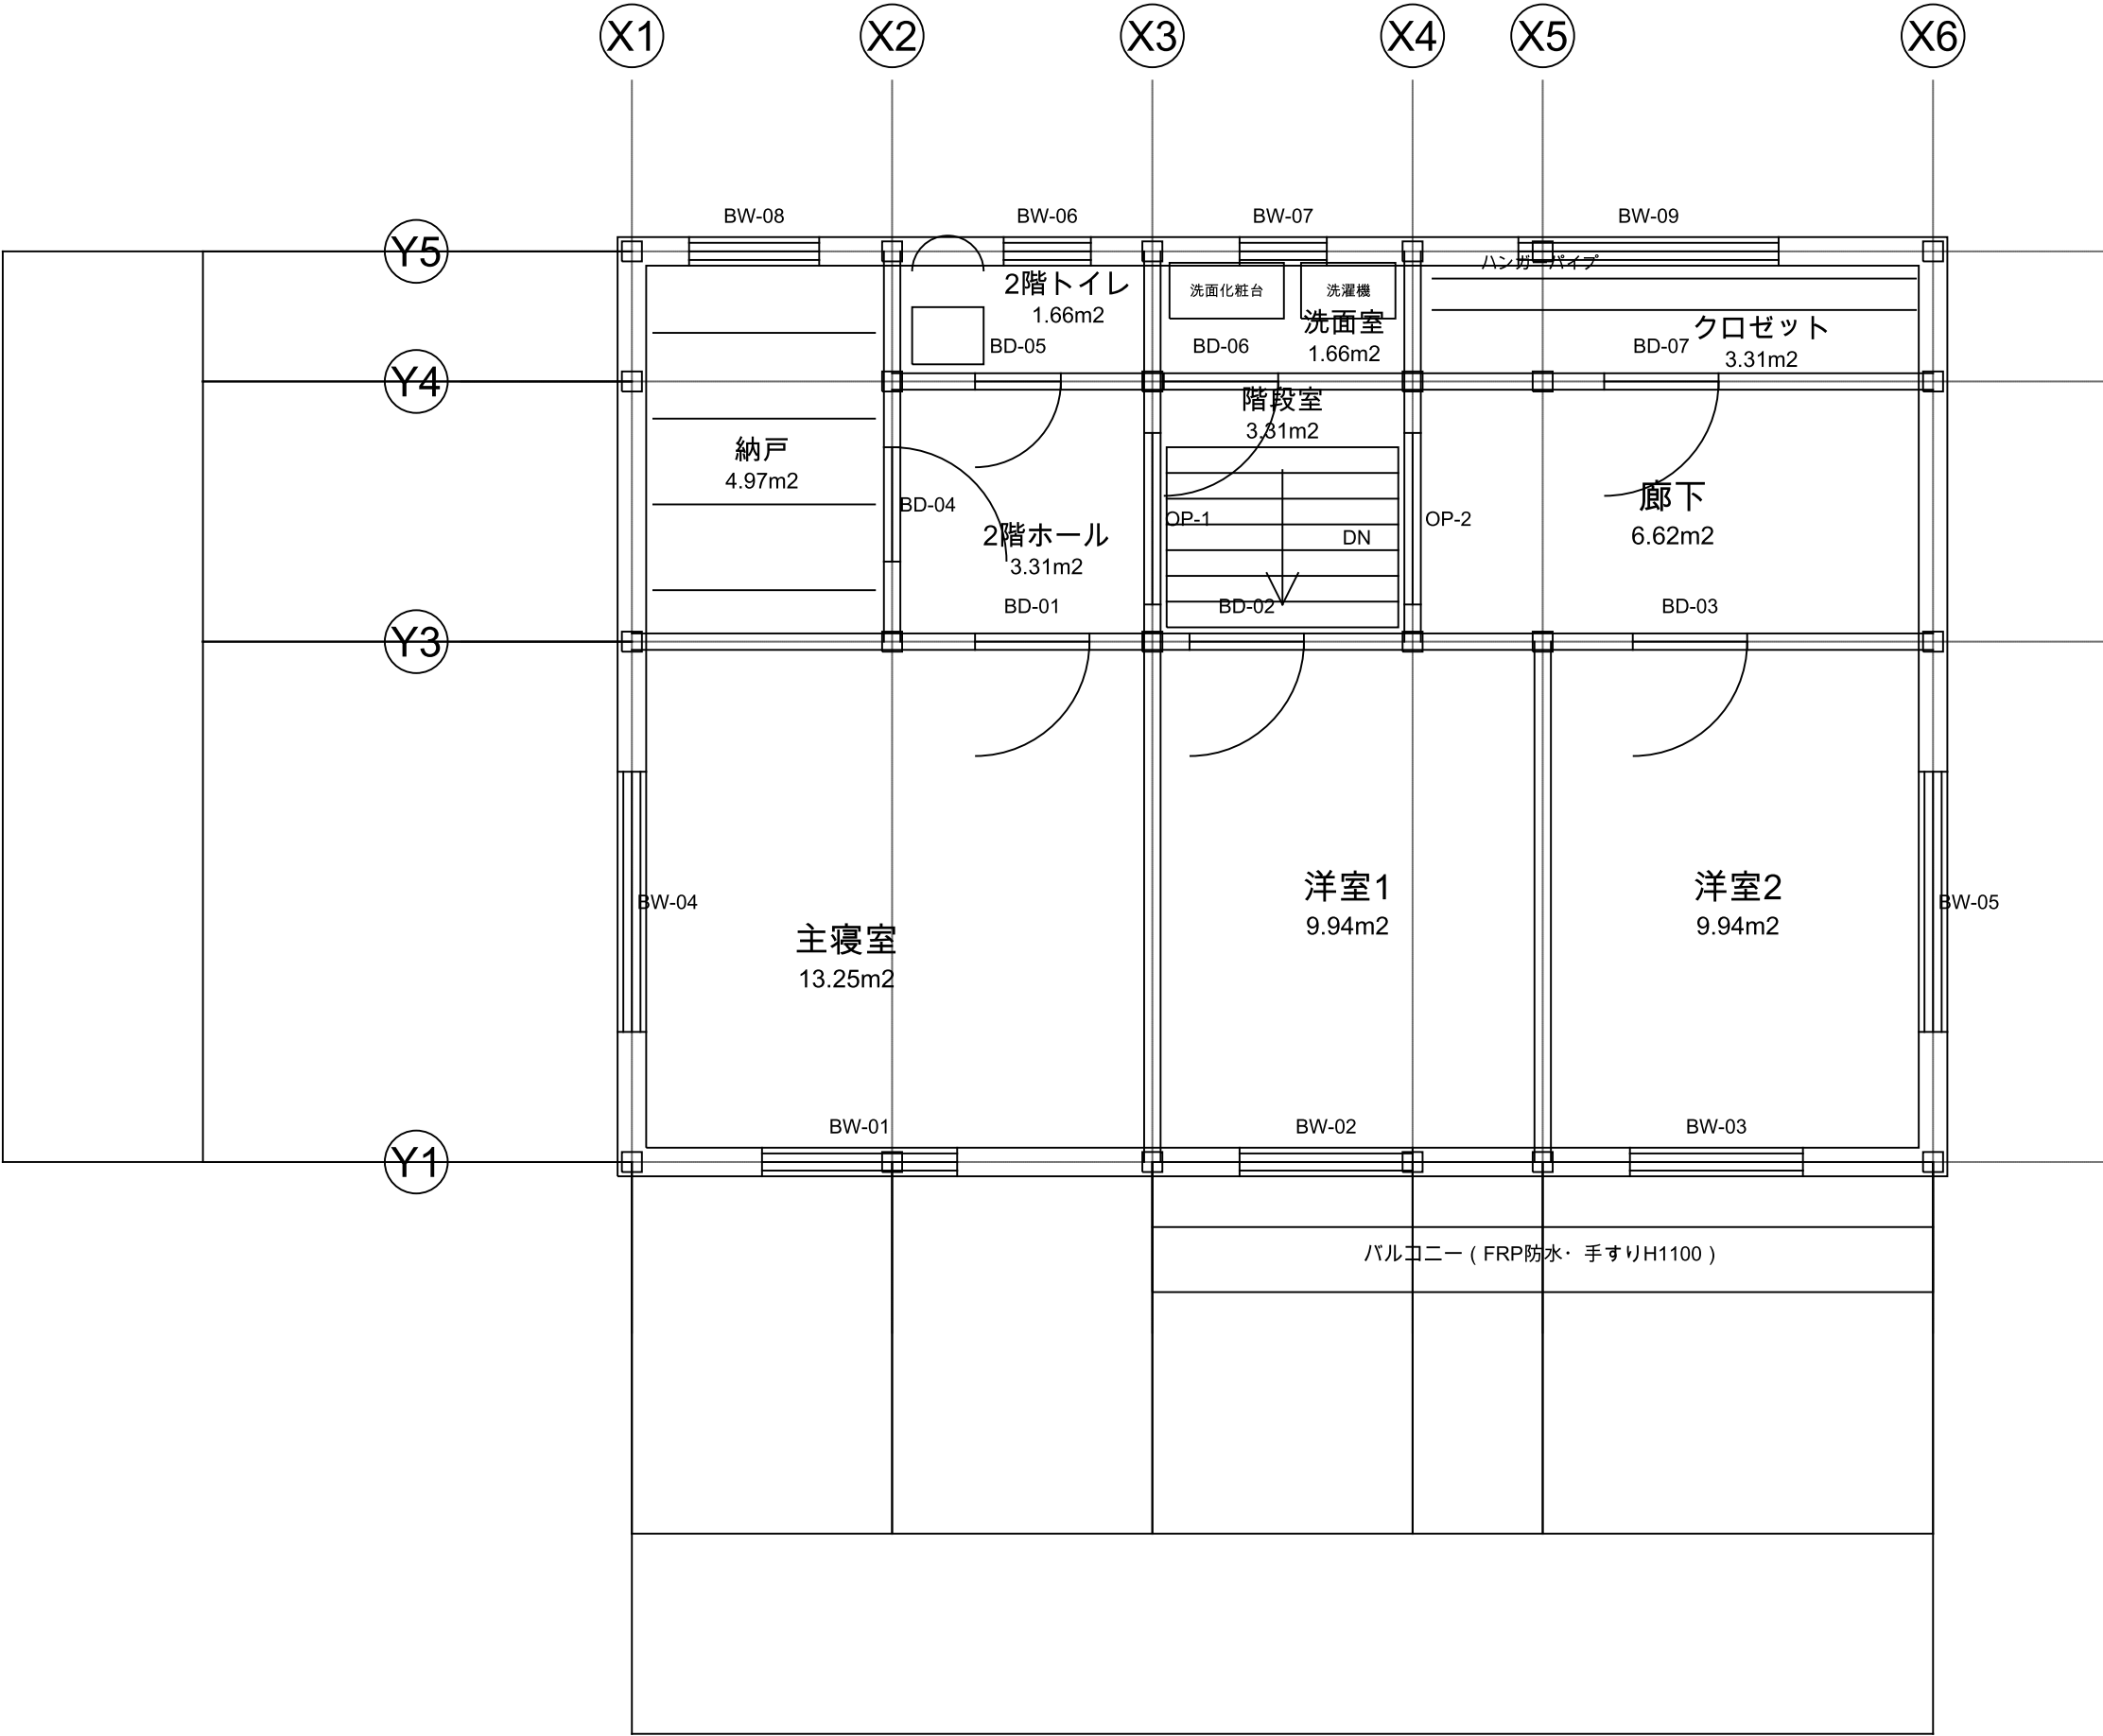


0 1 2 3 4 5(m)

構造 : 木造 枠組壁工法 (2×6)
床面積 : 57.97 m²

2階平面図	
設計者	株式会社 Design RAVO
発注者	株式会社 新昭和 (親会社)
作成日	2026-09-14
縮 尺	S=1:50
図面番号	A-04

立面図 (南・ 東・ 北・ 西) S=1:100

新昭和グループ 標準仕様 2×6 戸建住宅 参考設計図書
WITH EARTH / ウィザースホーム仕様 木造2階建 新築工事

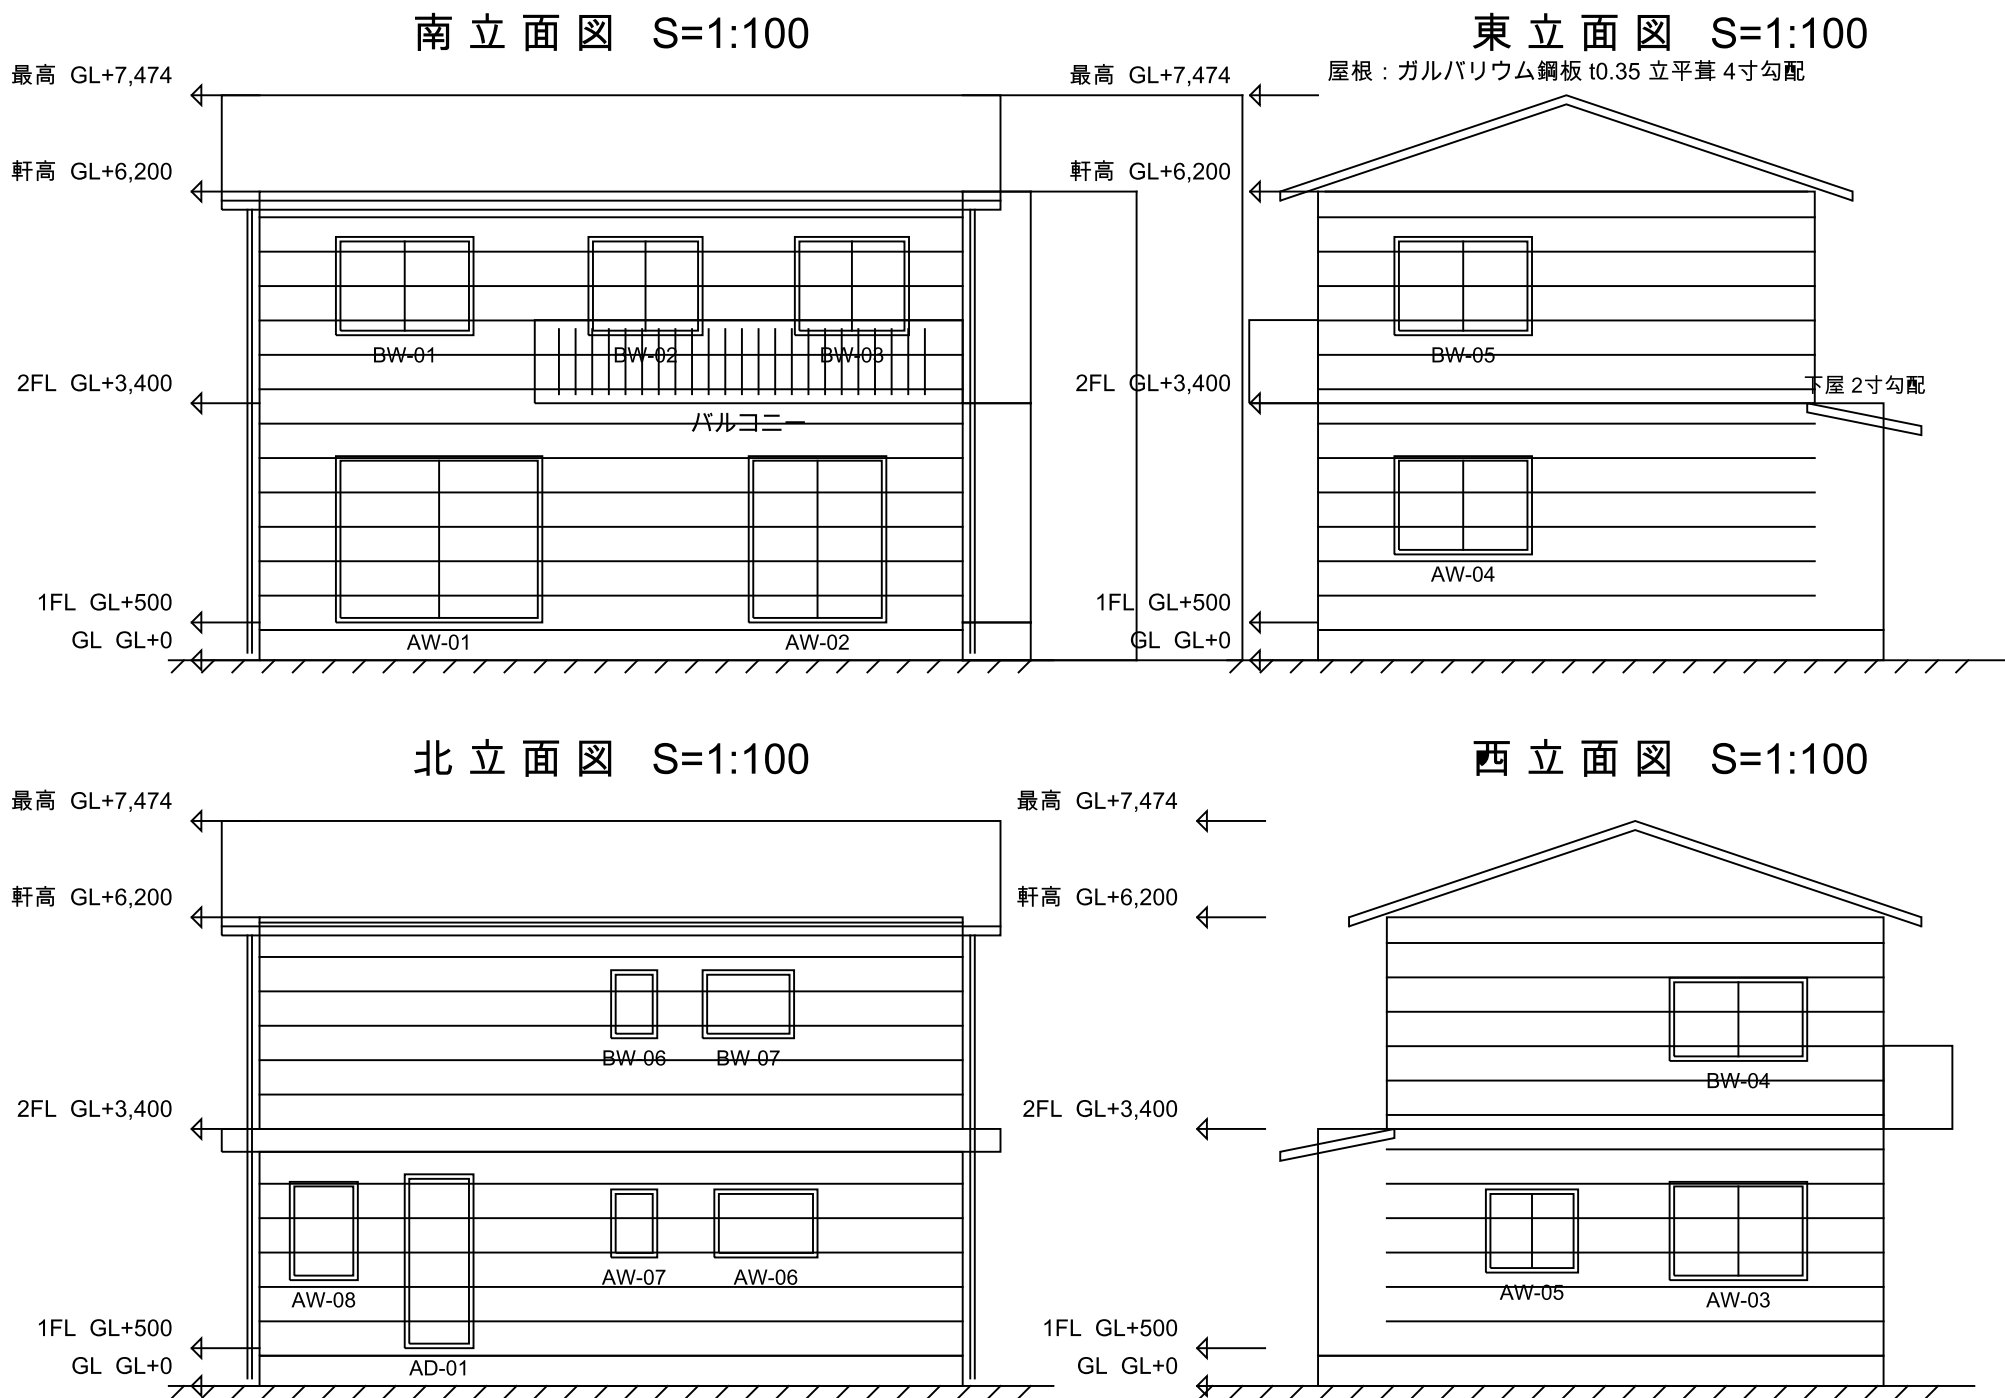

- 【外部仕上げ】
- 屋根：ガルバリウム鋼板 t0.35 立平葺 (主屋根 4寸勾配)
下屋は2寸勾配とする
 - 外壁：乾式外装タイル 45二丁 / 通気胴縁 t18
透湿防水シート / 構造用合板 t9
 - 軒裏：けい酸カルシウム板 t6 準不燃・ 軒天換気材
とい：たてとい φ60 / 軒どい 半丸105
 - 建具：樹脂サッシ + Low-E複層ガラス (アルゴン入)

- 【高さ関係】
- 最高の高さ GL+7,474
 - 軒の高さ GL+6,200
 - 1階階高 2,900 / 2階階高 2,800
 - 天井高 2,400 (浴室を除く)

- 【見方】
- 北立面は北から見た姿 (図の右が西)。
 - 西立面は西から見た姿 (図の右が南)。
 - 2階を南へ 910 後退させ、1階の張出し部に下屋を架けている。

- 【共通注記】
1. 寸法の単位は mm。特記なき限り通り芯 (壁芯) 寸法とする。
 2. 構造は木造2階建 枠組壁工法 (2×6) とし、親会社 株式会社 新昭和「ウィザースホーム」の標準工法 (モノコック構造) に準拠する。
 3. 本図面集は参考プラン (架空案件) である。実在の敷地・ 施主ではない。実施設計にあたっては敷地条件・ 地盤調査結果・ 各種申請の指導事項を反映すること。
 4. 法適合の検算結果は 03_計算書「法令適合検算書」を参照。同書で『未検算』とした項目は合格ではない。

軒の高さ：GL+6,200
最高の高さ：GL+7,474

立面図 (南・ 東・ 北・ 西)	
設計者	株式会社 Design RAVO
発注者	株式会社 新昭和 (親会社)
作成日	2026-09-14
縮 尺	S=1:100
図面番号	A-05

断面図 (A-A'・ B-B') S=1:100

新昭和グループ 標準仕様 2×6 戸建住宅 参考設計図書
WITH EARTH / ウィザースホーム仕様 木造2階建 新築工事

【断熱仕様】
天井：吹込みグラスウール 18K t300 (ブローイング)
外壁：高性能グラスウール 16K t140
 (2×6 たて枠 38×140 の内側に充填)
床 ：押出法ポリスチレンフォーム 3種 t90
開口：樹脂サッシ+Low-E複層ガラス (アルゴン入)


【構造の要点】
2階床根太：2×10 (38×235) @455
軒桁・頭つなぎ：2×6 二丁合わせ
基礎：布基礎 (立上り t150 H450 / フーチング W600)

【高さ】
1階階高 2,900 / 2階階高 2,800
軒高 GL+6,200 / 最高 GL+7,474


【B-B' の見方】
棟と平行に切っているため、切断面の屋根は水平に見える。
棟 (GL+7,474) は切断面の向こう側にあり、破線で示す。

【共通注記】
1. 寸法の単位は mm。特記なき限り通り芯 (壁芯) 寸法とする。
2. 構造は木造2階建 枠組壁工法 (2×6) とし、親会社 株式会社
新昭和「ウィザースホーム」の標準工法 (モノコック構造) に
準拠する。
3. 本図面集は参考プラン (架空案件) である。実在の敷地・施主
ではない。実施設計にあたっては敷地条件・地盤調査結果・
各種申請の指導事項を反映すること。
4. 法適合の検算結果は 03_計算書「法令適合検算書」を参照。
同書で『未検算』とした項目は合格ではない。

A-A' 断面図 S=1:100

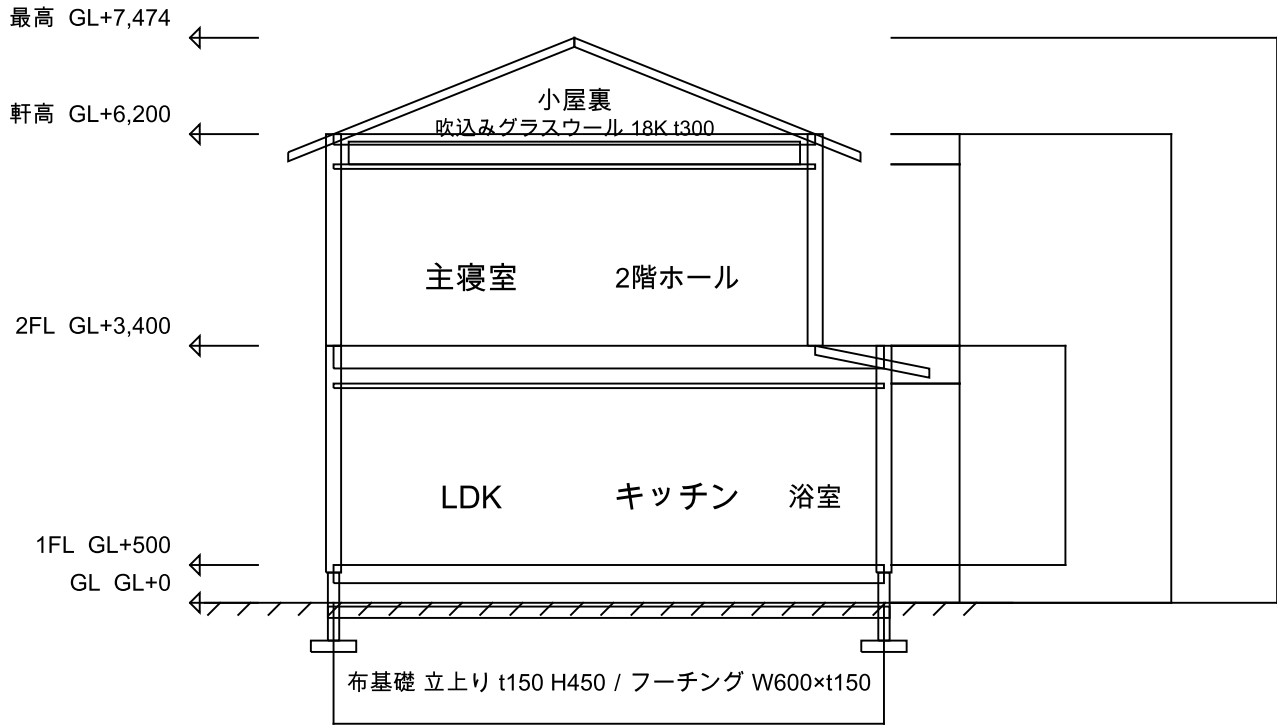

B-B' 断面図 S=1:100


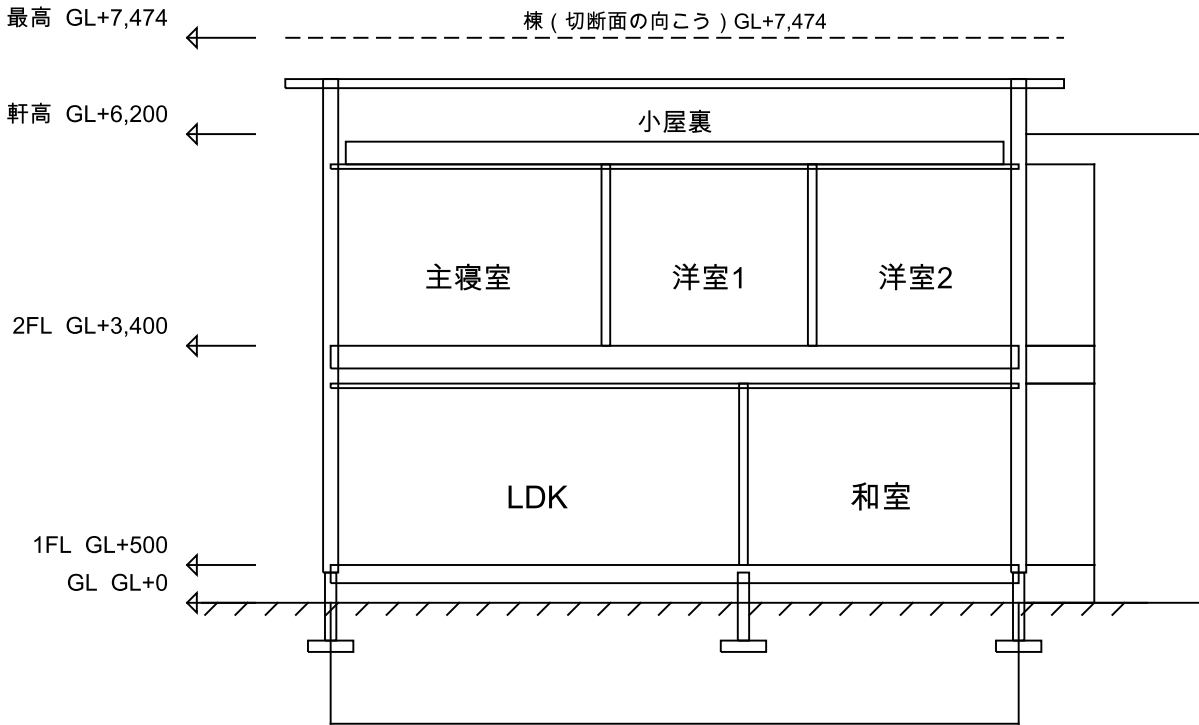


B-B' : Y=1,820 通り (東西方向)
A-A' : X=2,730 通り (南北方向)

断面図 (A-A'・ B-B')	
設計者	株式会社 Design RAVO
発注者	株式会社 新昭和 (親会社)
作成日	2026-09-14
縮 尺	S=1:100
図面番号	A-06

屋根伏図 S=1:50

新昭和グループ 標準仕様 2×6 戸建住宅 参考設計図書
WITH EARTH / ウィザースホーム仕様 木造2階建 新築工事

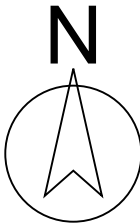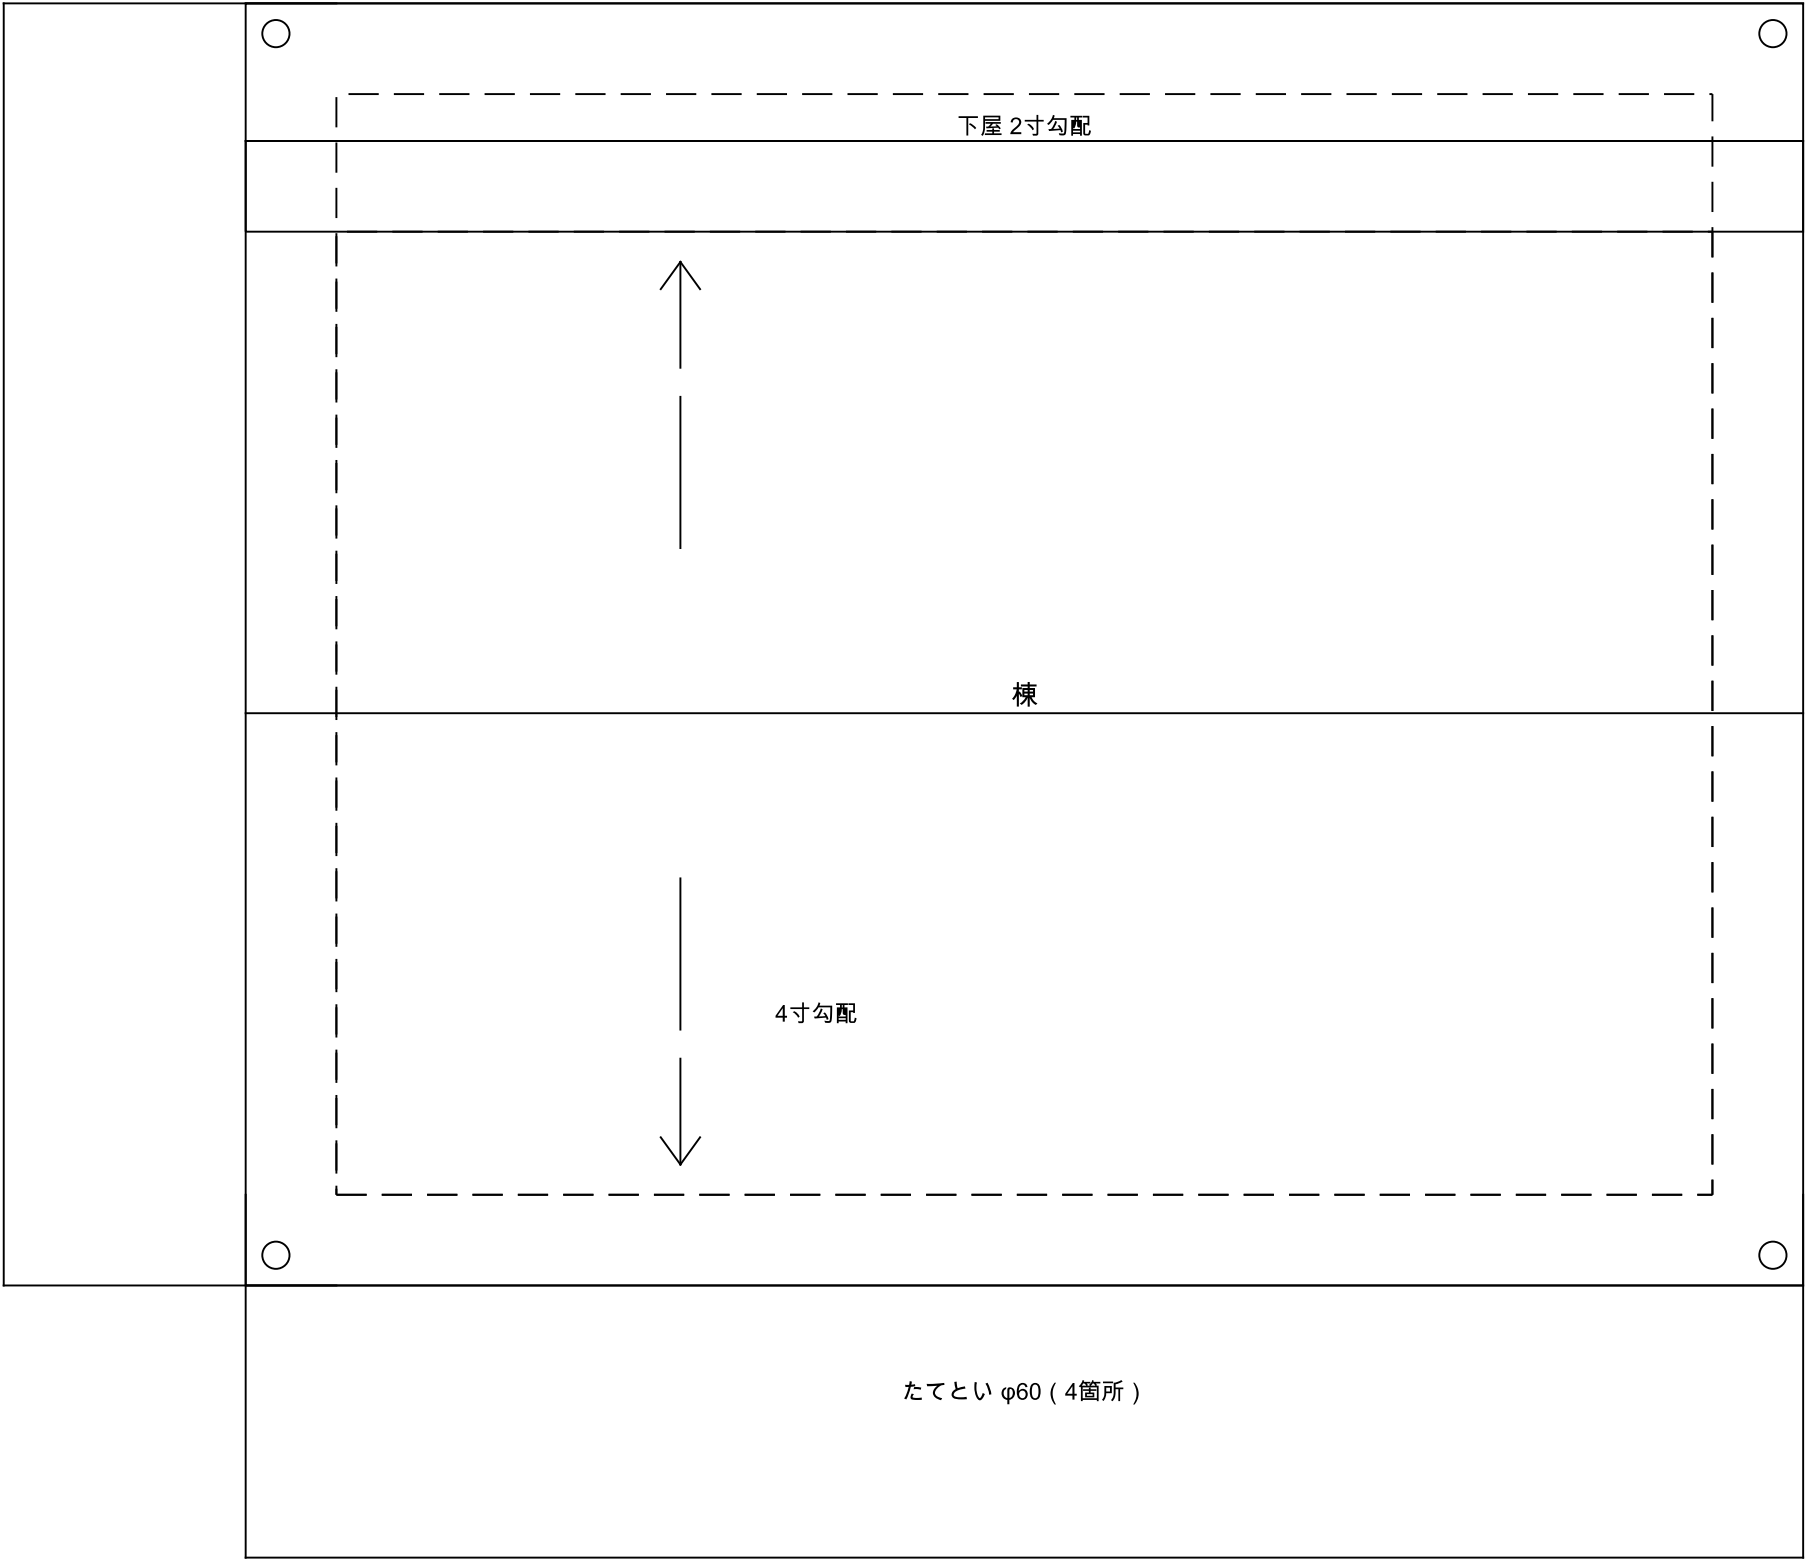

【屋根仕様】
ガルバリウム鋼板 t0.35 立平葺
改質アスファルトルーフィング / 構造用合板 t12
主屋根 4寸勾配 (切妻・棟は東西方向)
下屋 2寸勾配 (北側 1階張り出し部)
軒の出・ けらば出とも 600

【とい】
軒どい 半丸105 / たてとい φ60 (4箇所)

【換気】
軒天換気材を軒裏全長に設ける。
小屋裏換気は天井面積の 1/250 以上を確保すること
(実面積の確定は実施設計時)。

【共通注記】
1. 寸法の単位は mm。特記なき限り通り芯 (壁芯) 寸法とする。
2. 構造は木造2階建 枠組壁工法 (2×6) とし、親会社 株式会社
新昭和「ウィザースホーム」の標準工法 (モノコック構造) に
準拠する。
3. 本図面集は参考プラン (架空案件) である。実在の敷地・施主
ではない。実施設計にあたっては敷地条件・地盤調査結果・
各種申請の指導事項を反映すること。
4. 法適合の検算結果は 03_計算書「法令適合検算書」を参照。
同書で『未検算』とした項目は合格ではない。

屋 根 伏 図 S=1:50

軒の出 : 600
屋根勾配 : 主屋根 4寸 / 下屋 2寸

屋根伏図	
設計者	株式会社 Design RAVO
発注者	株式会社 新昭和 (親会社)
作成日	2026-09-14
縮 尺	S=1:50
図面番号	A-07

建具表 S=1:50

新昭和グループ 標準仕様 2×6 戸建住宅 参考設計図書
WITH EARTH / ウィザースホーム仕様 木造2階建 新築工事

建 具 表

符 号	名 称	呼 称 寸 法	材 質 ・ 仕 様	数 量	備 考
AD-01	玄関ドア	W910×H2300	アルミ断熱玄関ドア / 電気錠・ Low-E複層ガラス	1	K1.5仕様
AW-01	掃出し窓	W2730×H2200	樹脂サッシ / Low-E複層ガラス (アルゴン入)	1	LDK 南面
AW-02	掃出し窓	W1820×H2200	樹脂サッシ / Low-E複層ガラス (アルゴン入)	1	和室 南面
AW-03	引違い窓	W1820×H1300	樹脂サッシ / Low-E複層ガラス (アルゴン入)	1	LDK 西面
AW-04	引違い窓	W1820×H1300	樹脂サッシ / Low-E複層ガラス (アルゴン入)	1	和室 東面
AW-05	引違い窓	W1620×H1100	樹脂サッシ / Low-E複層ガラス (アルゴン入)	1	キッチン 西面・ 採光確保
AW-06	横すべり出し窓	W1365×H900	樹脂サッシ / Low-E複層ガラス	1	浴室 北面・ 型板
AW-07	縦すべり出し窓	W610×H900	樹脂サッシ / Low-E複層ガラス	1	トイレ 北面・ 型板
AW-08	FIX窓	W900×H1300	樹脂サッシ / Low-E複層ガラス	1	玄関 北面
SD-01	室内引戸 (3枚)	W1820×H2000	既製建具 / ソフトクローズ	1	LDK⇔キッチン
SD-02	和室引違戸	W1820×H1800	和室用引戸 (襖仕上)	1	LDK⇔和室
SD-03	浴室入口引戸	W910×H2000	樹脂製・ 防水仕様	1	洗面脱衣⇔浴室
SD-04	室内引戸	W910×H2000	既製建具 / ソフトクローズ	1	キッチン⇔洗面脱衣
DR-01	室内開き戸	W800×H2000	既製建具 / レバーハンドル	1	玄関ホール⇔階段室
DR-02	室内開き戸	W800×H2000	既製建具 / レバーハンドル	1	洗面脱衣⇔トイレ前
DR-04	トイレ開き戸	W800×H2000	既製建具 / 表示錠付	1	1階トイレ
BW-01	引違い窓	W1365×H1300	樹脂サッシ / Low-E複層ガラス (アルゴン入)	1	主寝室 南面
BW-02	引違い窓	W1210×H1300	樹脂サッシ / Low-E複層ガラス (アルゴン入)	1	洋室1 南面
BW-03	引違い窓	W1210×H1300	樹脂サッシ / Low-E複層ガラス (アルゴン入)	1	洋室2 南面
BW-04	引違い窓	W1820×H1100	樹脂サッシ / Low-E複層ガラス (アルゴン入)	1	主寝室 西面
BW-05	引違い窓	W1820×H1100	樹脂サッシ / Low-E複層ガラス (アルゴン入)	1	洋室2 東面
BW-06	縦すべり出し窓	W610×H900	樹脂サッシ / 型板ガラス	1	2階トイレ 北面
BW-07	縦すべり出し窓	W610×H900	樹脂サッシ / 型板ガラス	1	洗面室 北面
BW-08	横すべり出し窓	W910×H900	樹脂サッシ / Low-E複層ガラス	1	納戸 北面
BW-09	横すべり出し窓	W1820×H900	樹脂サッシ / Low-E複層ガラス	1	クロゼット 北面
BD-01	室内開き戸	W800×H2000	既製建具 / レバーハンドル	1	2階ホール⇔主寝室
BD-02	室内開き戸	W800×H2000	既製建具 / レバーハンドル	1	階段室⇔洋室1
BD-03	室内開き戸	W800×H2000	既製建具 / レバーハンドル	1	廊下⇔洋室2
BD-04	折戸	W800×H2000	既製建具	1	2階ホール⇔納戸
BD-05	トイレ開き戸	W600×H2000	既製建具 / 表示錠付	1	2階トイレ
BD-06	室内開き戸	W800×H2000	既製建具 / レバーハンドル	1	階段室⇔洗面室
BD-07	クロゼット折戸	W800×H2000	既製建具	1	廊下⇔クロゼット
OP-1	開口 (建具なし)	W1200×H2000	開口のみ (三方枠)	1	階段室⇔2階ホール
OP-2	開口 (建具なし)	W1200×H2000	開口のみ (三方枠)	1	階段室⇔廊下

【建具の共通仕様】
外部建具：樹脂サッシ / Low-E複層ガラス (アルゴンガス入)
水切り・ シーリングは標準仕様による。
玄関ドア：アルミ断熱ドア (K1.5仕様) / 電気錠
内部建具：既製建具。引戸はソフトクローズ付とする。
浴室入口：樹脂製・ 防水仕様
トイレ ：表示錠付

【符号の付け方】
AW / AD ... 1階の外部建具 (窓・ 玄関)
BW ... 2階の外部建具
SD / DR ... 1階の内部建具 (引戸 / 開き戸)
BD ... 2階の内部建具
OP ... 建具を設けない開口 (三方枠のみ)

【この表の作り方】
平面図に描いた建具と、この表の行が一対一に対応していることを
作成時に機械で突き合わせています (図面にあって表に無い建具、
表にあって図面に無い建具はいずれも 0 件)。

【共通注記】
1. 寸法の単位は mm。特記なき限り通り芯 (壁芯) 寸法とする。
2. 構造は木造2階建 枠組壁工法 (2×6) とし、親会社 株式会社
新昭和「ウィザースホーム」の標準工法 (モノコック構造) に
準拠する。
3. 本図面集は参考プラン (架空案件) である。実在の敷地・ 施主
ではない。実施設計にあたっては敷地条件・ 地盤調査結果・
各種申請の指導事項を反映すること。
4. 法適合の検算結果は 03_計算書「法令適合検算書」を参照。
同書で『未検算』とした項目は合格ではない。

建具数：34 件

建具表	
設計者	株式会社 Design RAVO
発注者	株式会社 新昭和 (親会社)
作成日	2026-09-14
縮 尺	S=1:50
図面番号	A-08

仕上表 S=1:50

新昭和グループ 標準仕様 2×6 戸建住宅 参考設計図書
WITH EARTH / ウィザースホーム仕様 木造2階建 新築工事

仕 上 表

■ 外 部 仕 上

部 位	仕 様
屋 根	ガルバリウム鋼板 t0.35 立平葺 / 改質アスファルトルーフィング / 構造用合板 t12
外 壁	乾式外装タイル 45ニ丁 / 通気胴縁 t18 / 透湿防水シート / 構造用合板 t9
軒 裏	けい酸カルシウム板 t6 準不燃 / 軒天換気材
と い	塩ビ製 たてとい φ60 / 軒どい 半丸105
基 礎	鉄筋コンクリート造 布基礎 (一体打ち) / 立上り t150 H450 モルタル金ゴテ
バルコニー	FRP防水 / アルミ手すり H1100
建 具	樹脂サッシ / Low-E複層ガラス (アルゴンガス入)

■ 内 部 仕 上

室 名	床	壁	天 井	天井高
LDK	複合フローリング t12	ビニルクロス / PB t12.5	ビニルクロス / PB t9.5	2,400
和室	畳 t55 (縁付)	ビニルクロス / PB t12.5	和風クロス / PB t9.5	2,400
キッチン	複合フローリング t12	キッチンパネル + ビニルクロス	ビニルクロス / PB t9.5	2,400
玄関・ホール	磁器質タイル 300角 / 框 集成材	ビニルクロス / PB t12.5	ビニルクロス / PB t9.5	2,400
洗面脱衣室	クッションフロア t1.8	ビニルクロス (防カビ) / PB t12.5	ビニルクロス / PB t9.5	2,400
浴室	システムバス 1618 (床・壁・天井とも製品標準仕)		同左	2,100
トイレ	クッションフロア t1.8	ビニルクロス (消臭) / PB t12.5	ビニルクロス / PB t9.5	2,400
主寝室・洋室1・ 2	複合フローリング t12	ビニルクロス / PB t12.5	ビニルクロス / PB t9.5	2,400
納戸・クロゼット・廊下	複合フローリング t12	ビニルクロス / PB t12.5	ビニルクロス / PB t9.5	2,400
階段室	集成材 段板 / ノンスリップ	ビニルクロス / PB t12.5	ビニルクロス / PB t9.5	—

■ 断 熱 仕 様

部 位	断 熱 仕 様
天 井	吹込みグラスウール 18K t300 (ブローイング工法)
外 壁	高性能グラスウール 16K t140 (2×6 たて枠内充填)
床 (1階)	押出法ポリスチレンフォーム 3種 t90
開口部	樹脂サッシ + Low-E複層ガラス (アルゴンガス入)

■ 設 備 ・ 環 境 に か か る 仕 様

項 目	仕 様
換 気	24時間換気 (第3種) 常時運転。設計風量は居室ごとに気積×0.5回/h を5 m³/h 単位で切り上げ。
床 下 換 気	基礎パッキン (全周換気)。壁長さ5m あたり有効面積 375 cm²
小屋裏換気	軒天換気材による。天井面積の 1/250 以上を確保すること
シックハウス	内装仕上げは F☆☆☆☆ のみ。クロルピリホスの添加・使用なし
階 段	住宅の階段。蹴上げ 207.1 / 踏面 225 / 有効幅 780 / 手すり H850 (片側)

【仕上げの考え方】

親会社 株式会社新昭和「ウィザースホーム」の標準仕様に合わせています。外壁タイル・高断熱 (天井 t300 吹込み、外壁 2×6 たて枠内 t140 充填) は標準装備の扱いです。

【ご確認をお願いしたい事項】

外皮性能 (UA値・ ηAC値) の計算には、採用するサッシと玄関ドアの熱貫流率 (製品値) が必要です。製品が確定していないため、省エネ基準の適合判定は『未検算』としています。(2025年4月以降、原則としてすべての新築建築物で省エネ基準への適合が義務付けられています。)

【火気使用室の換気】

調理機器の種類 (ガス / IH) が確定していないため、令第20条の3の判定は行っていません。機器が決まり次第、算定します。

【共通注記】


- 寸法の単位は mm。特記なき限り通り芯 (壁芯) 寸法とする。
- 構造は木造2階建 枠組壁工法 (2×6) とし、親会社 株式会社新昭和「ウィザースホーム」の標準工法 (モノコック構造) に準拠する。
- 本図面集は参考プラン (架空案件) である。実在の敷地・施主ではない。実施設計にあたっては敷地条件・地盤調査結果・各種申請の指導事項を反映すること。
- 法適合の検算結果は 03_計算書「法令適合検算書」を参照。同書で『未検算』とした項目は合格ではない。

仕上表

設計者	株式会社 Design RAVO
発注者	株式会社 新昭和 (親会社)
作成日	2026-09-14
縮 尺	S=1:50
図面番号	A-09

基礎伏図 S=1:50

新昭和グループ 標準仕様 2×6 戸建住宅 参考設計図書
WITH EARTH / ウィザースホーム仕様 木造2階建 新築工事

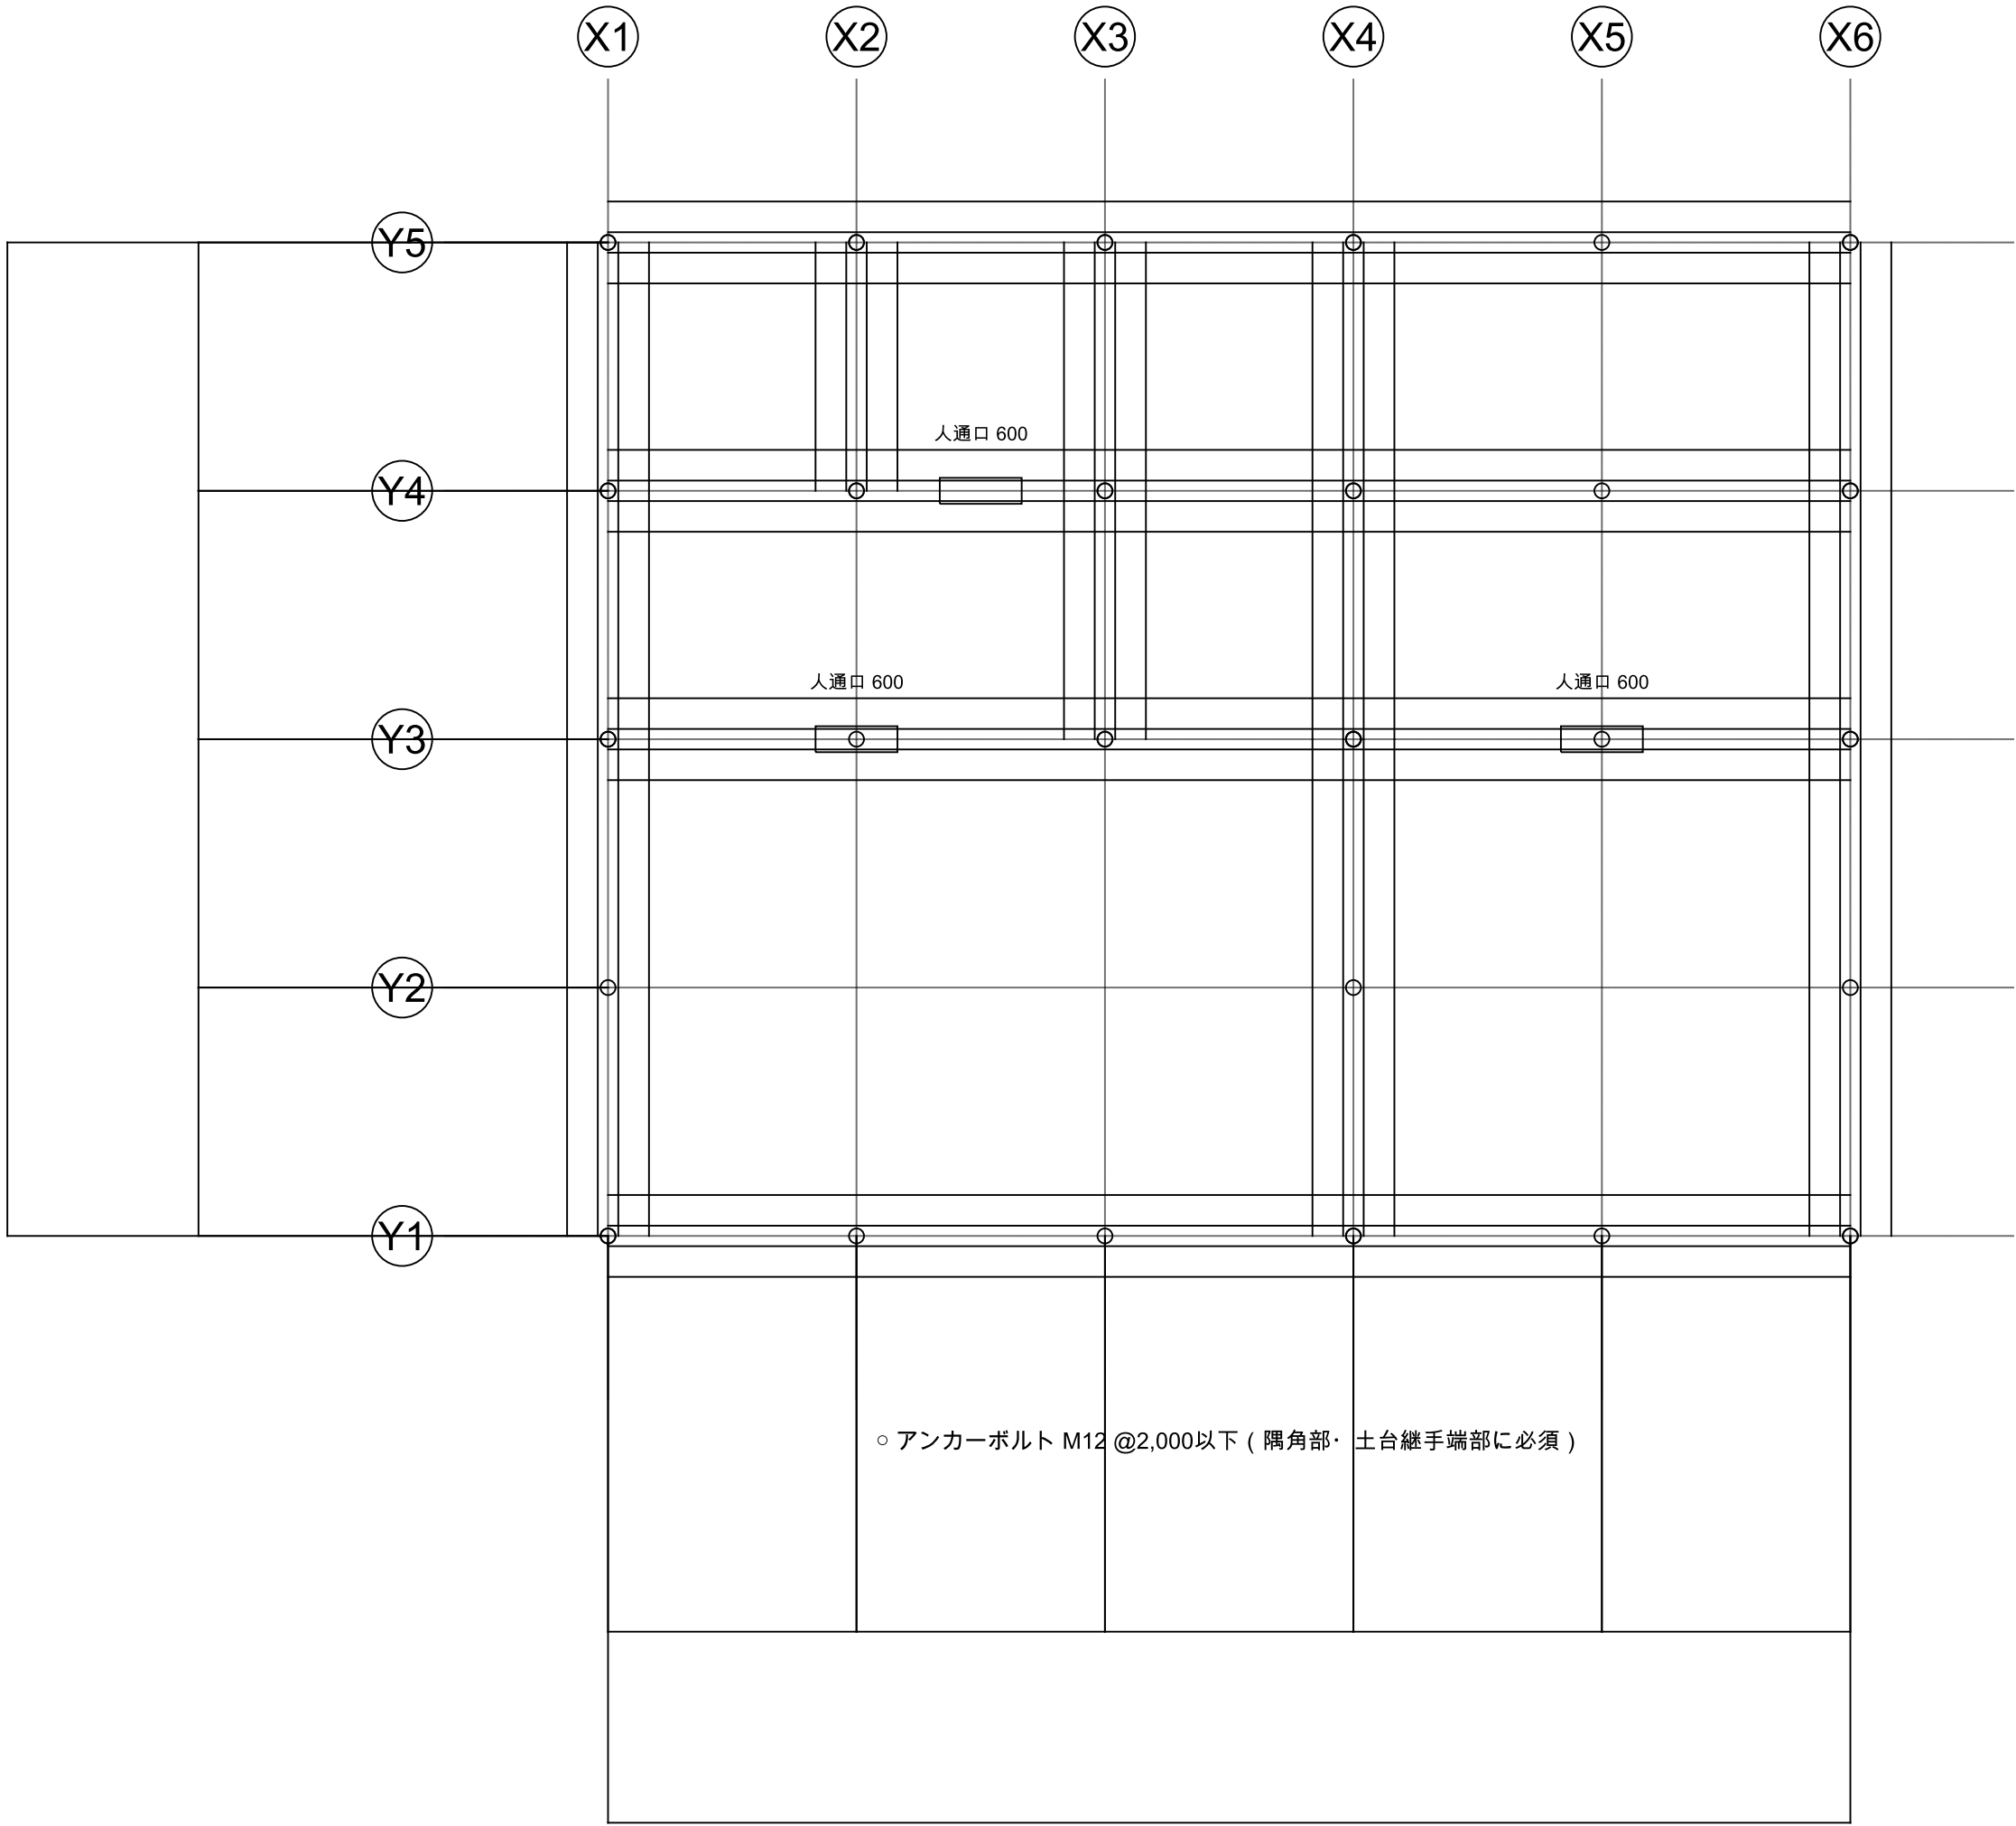

【基礎仕様】
形式 鉄筋コンクリート造 布基礎 (底盤: 立上り一体打ち)
立上り t150 × H450 (GL+400 / FL-100)
フーチング W600 × t150
配筋 立上り 主筋 D13 上下各1本 / 補強筋 D10 @300
底盤 D13 @200 シングル
かぶり 土に接する部分 60mm 以上
土間 防湿コンクリート t60 / 防湿フィルム t0.15
アンカーボルト M12 @2,000 以下
(隅角部・土台継手端部には必ず設ける)

【ご用意いただくもの】
地盤調査報告書 (許容応力度)。基礎が地盤に支えられるかの検定は、この値が無いと行えません。当方では作りません。

【共通注記】
1. 寸法の単位は mm。特記なき限り通り芯 (壁芯) 寸法とする。
2. 構造は木造2階建 枠組壁工法 (2×6) とし、親会社 株式会社 新昭和「ウィザースホーム」の標準工法 (モノコック構造) に準拠する。
3. 本図面集は参考プラン (架空案件) である。実在の敷地・施主ではない。実施設計にあたっては敷地条件・地盤調査結果・各種申請の指導事項を反映すること。
4. 法適合の検算結果は 03_計算書「法令適合検算書」を参照。同書で『未検算』とした項目は合格ではない。



立上り : t150 × H450
基礎形式 : 布基礎 (一体打ち)

基礎伏図	
設計者	株式会社 Design RAVO
発注者	株式会社 新昭和 (親会社)
作成日	2026-09-14
縮 尺	S=1:50
図面番号	S-01

基 礎 伏 図 S=1:50

床伏図 (1階・ 2階) S=1:100

新昭和グループ 標準仕様 2×6 戸建住宅 参考設計図書
WITH EARTH / ウィザースホーム仕様 木造2階建 新築工事

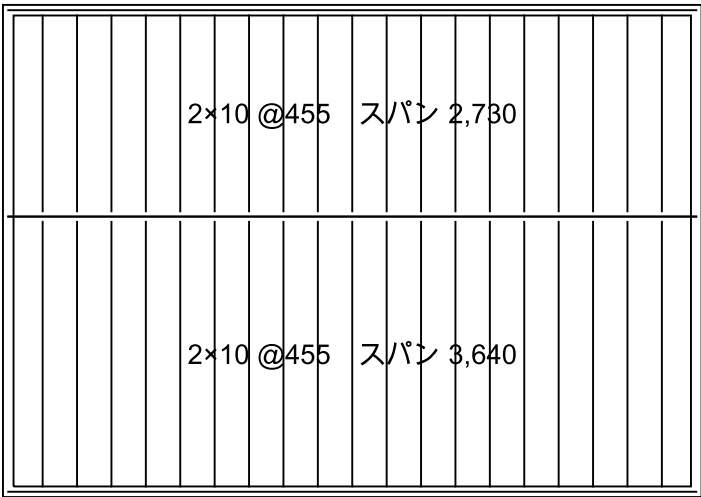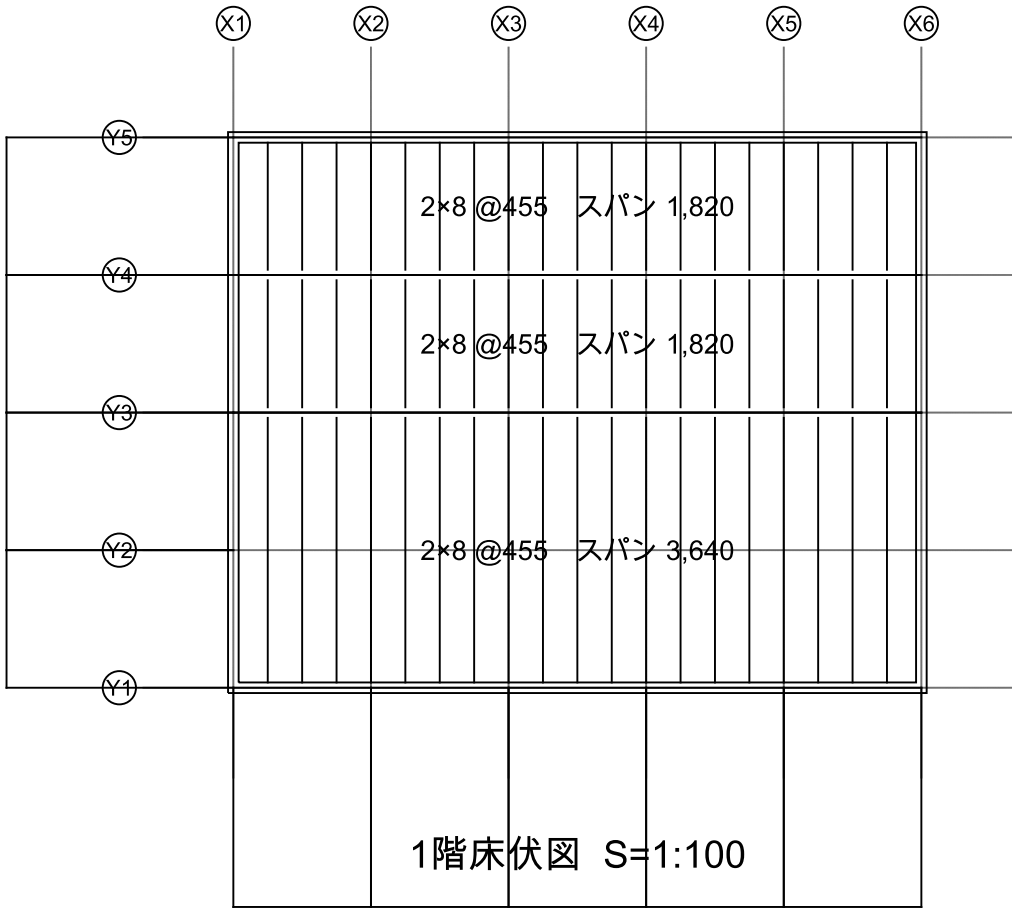

【床組】
1階 根太 2×8 (38×184) @455 床下地 構造用合板 t24
2階 根太 2×10 (38×235) @455 床下地 構造用合板 t24
端根太・側根太は根太と同寸とする。
開口部にはヘッダー (2×10 ニ丁合わせ) を設ける。
根太受け金物は釘打ち仕様 (CN 釘) に従う。

【材料】
枠組材 SPF 構造用製材 甲種 2級 (JAS)
釘 CN50 / CN75 / CN90 (枠組壁工法用)

【たわみの検定】
部材の曲げ・せん断・たわみの検定結果は 03_計算書
「構造計算書」に記載。ヤング係数 E は材料の等級区分
によるため、実施設計では材料証明書でご確認ください。


【共通注記】
1. 寸法の単位は mm。特記なき限り通り芯 (壁芯) 寸法とする。
2. 構造は木造2階建 枠組壁工法 (2×6) とし、親会社 株式会社
新昭和「ウィザースホーム」の標準工法 (モノコック構造) に
準拠する。
3. 本図面集は参考プラン (架空案件) である。実在の敷地・施主
ではない。実施設計にあたっては敷地条件・地盤調査結果・
各種申請の指導事項を反映すること。
4. 法適合の検算結果は 03_計算書「法令適合検算書」を参照。
同書で『未検算』とした項目は合格ではない。

2階床根太 : 2×10 (38×235) @455
1階床根太 : 2×8 (38×184) @455

床伏図 (1階・ 2階)	
設計者	株式会社 Design RAVO
発注者	株式会社 新昭和 (親会社)
作成日	2026-09-14
縮 尺	S=1:100
図面番号	S-02

小屋伏図 S=1:50

新昭和グループ 標準仕様 2×6 戸建住宅 参考設計図書
WITH EARTH / ウィザースホーム仕様 木造2階建 新築工事

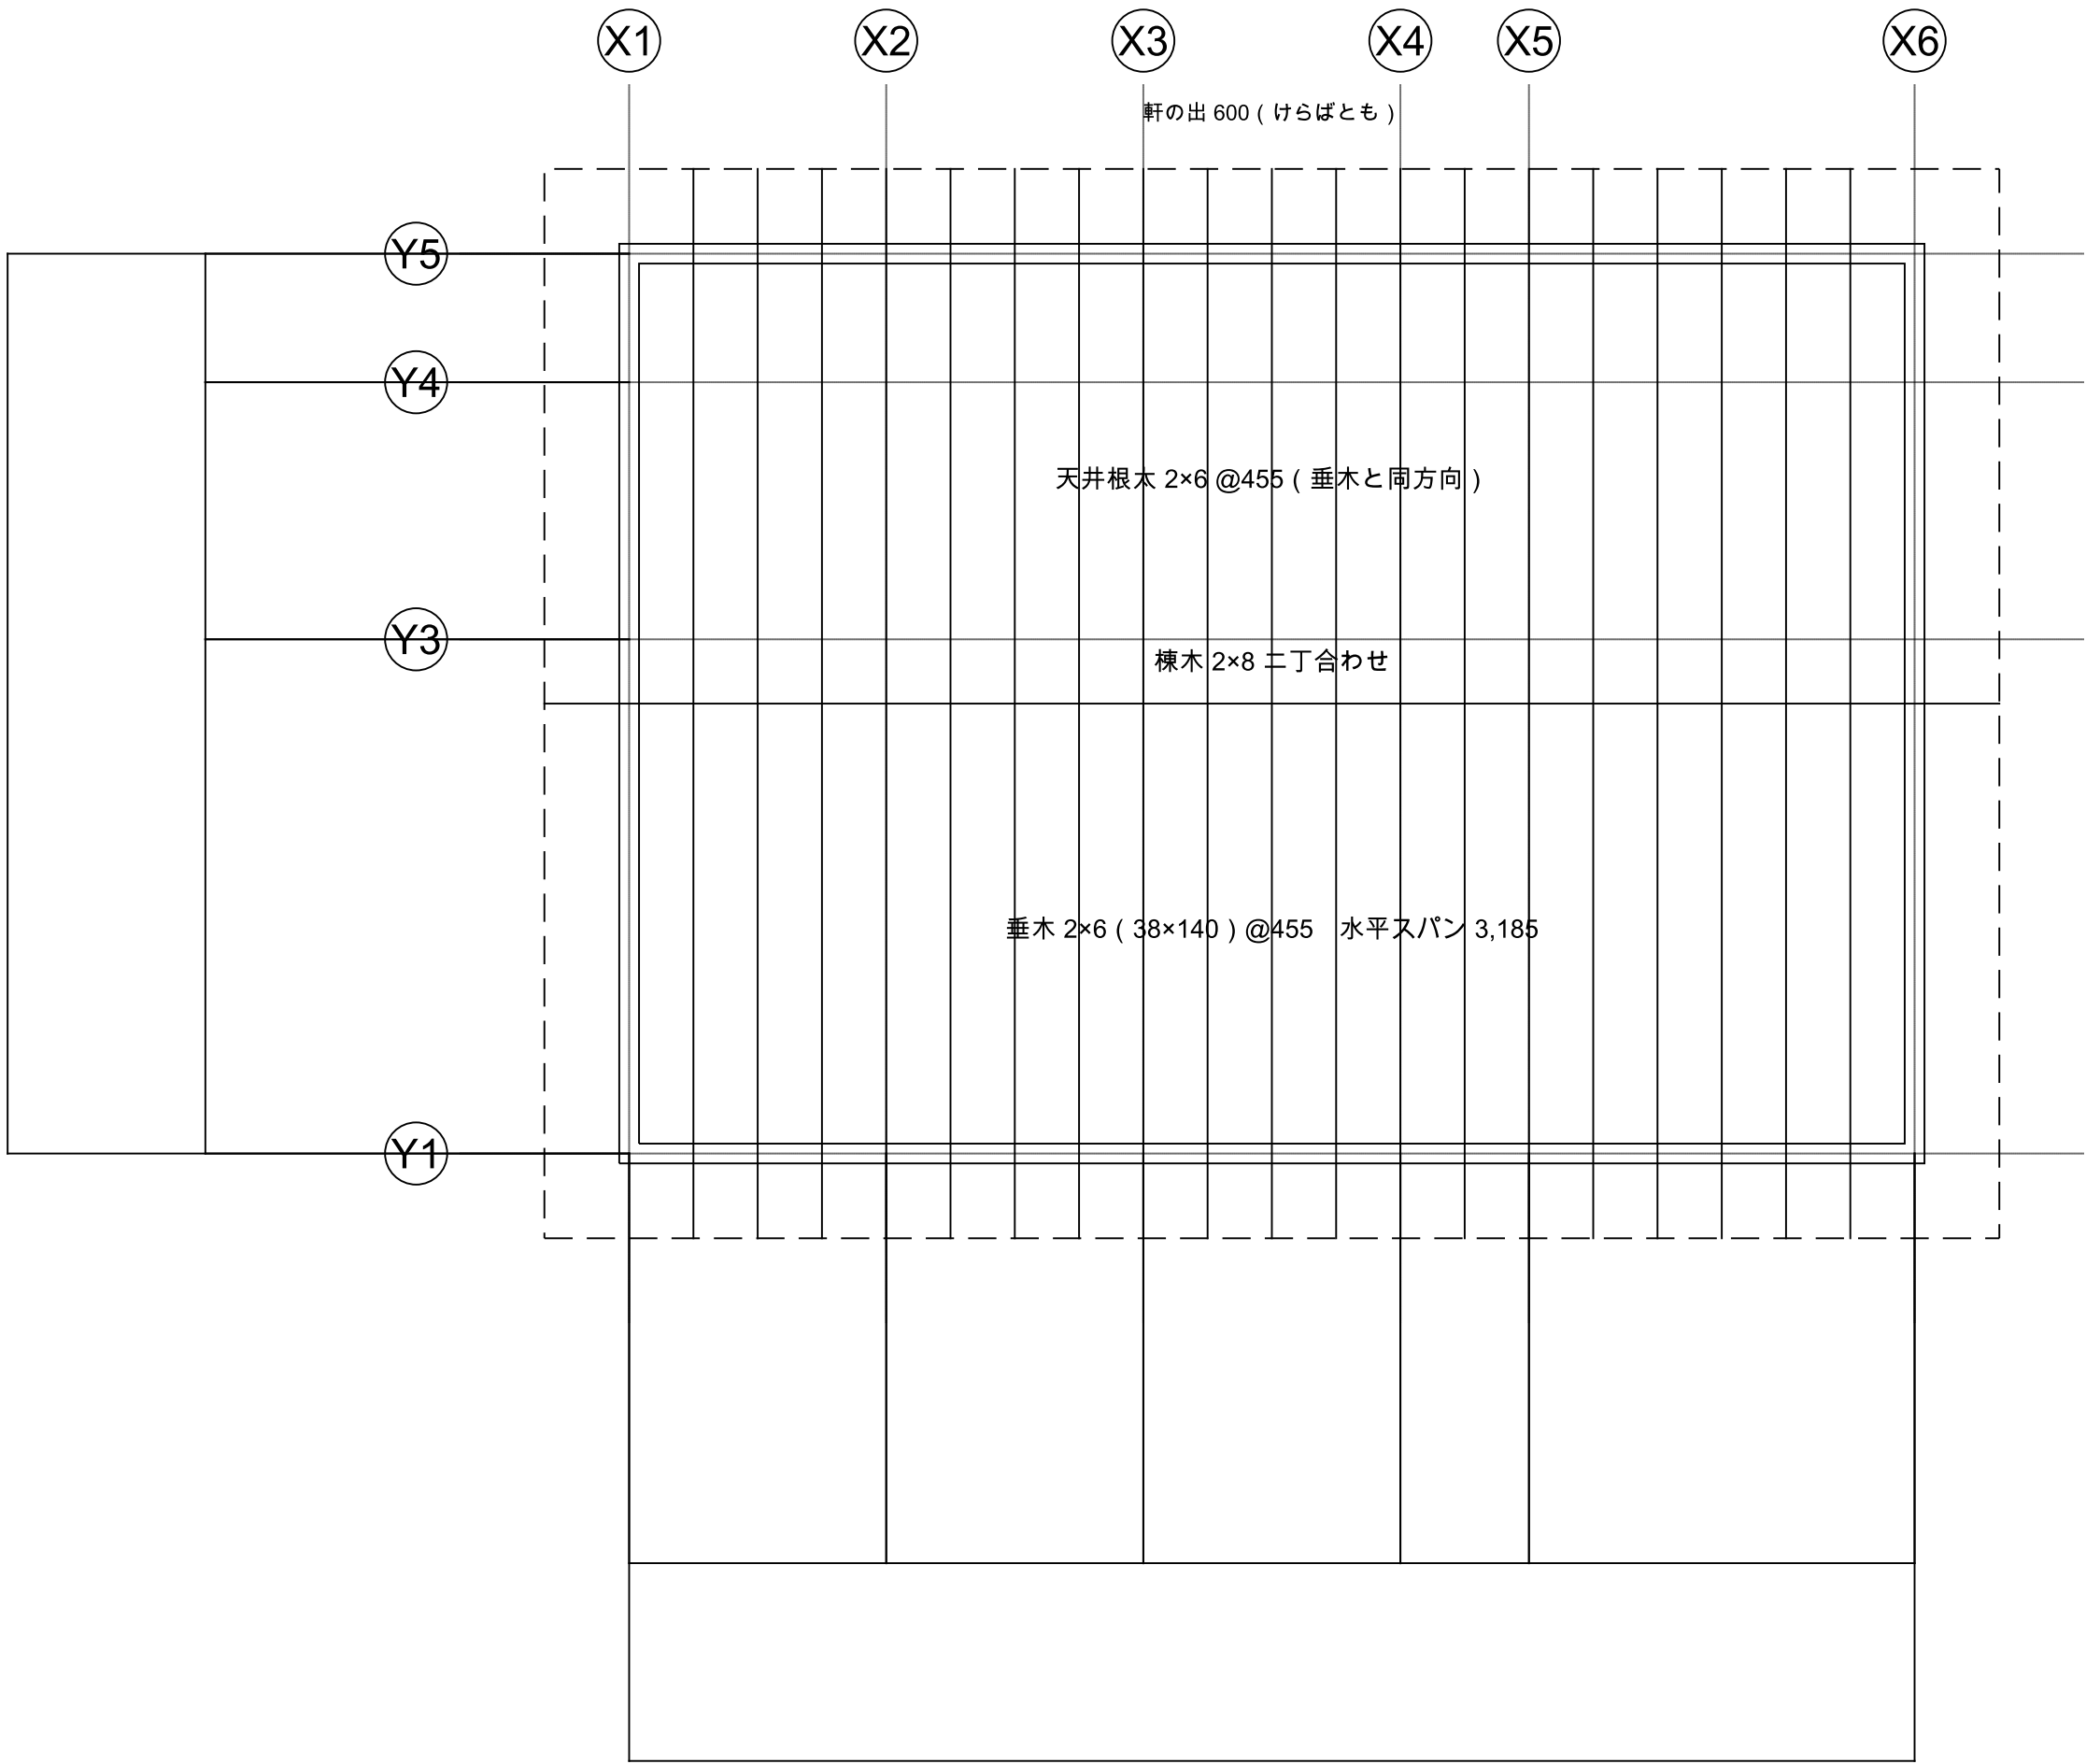

【小屋組】
垂木 2×6 (38×140) @455 水平スパン 3,185
棟木 2×8 二丁合わせ
天井根太 2×6 (38×140) @455
構造用合板 t12 (野地) / 改質アスファルトルーフィング
あおり止め金物を垂木・軒桁の取合いに全数設ける。

【小屋裏】
吹込みグラスウール 18K t300
軒天換気材により小屋裏換気を確保する。

【積雪・風について】
積雪時・暴風時の検定は、垂直積雪量 (特定行政庁が定める)
と基準風速 (告示第1454号) が確定してから行います。
これらは所在地で決まる値のため、当方で数値を作ることは
していません。03_計算書では『未検算』として開示しています。

【共通注記】
1. 寸法の単位は mm。特記なき限り通り芯 (壁芯) 寸法とする。
2. 構造は木造2階建 枠組壁工法 (2×6) とし、親会社 株式会社
新昭和「ウィザースホーム」の標準工法 (モノコック構造) に
準拠する。
3. 本図面集は参考プラン (架空案件) である。実在の敷地・施主
ではない。実施設計にあたっては敷地条件・地盤調査結果・
各種申請の指導事項を反映すること。
4. 法適合の検算結果は 03_計算書「法令適合検算書」を参照。
同書で『未検算』とした項目は合格ではない。


小 屋 伏 図 S=1:50

屋根勾配 : 4寸
垂木 : 2×6 (38×140) @455


小屋伏図	
設計者	株式会社 Design RAVO
発注者	株式会社 新昭和 (親会社)
作成日	2026-09-14
縮 尺	S=1:50
図面番号	S-03

耐力壁配置図 (1階・ 2階) S=1:100

新昭和グループ 標準仕様 2×6 戸建住宅 参考設計図書
WITH EARTH / ウィザースホーム仕様 木造2階建 新築工事

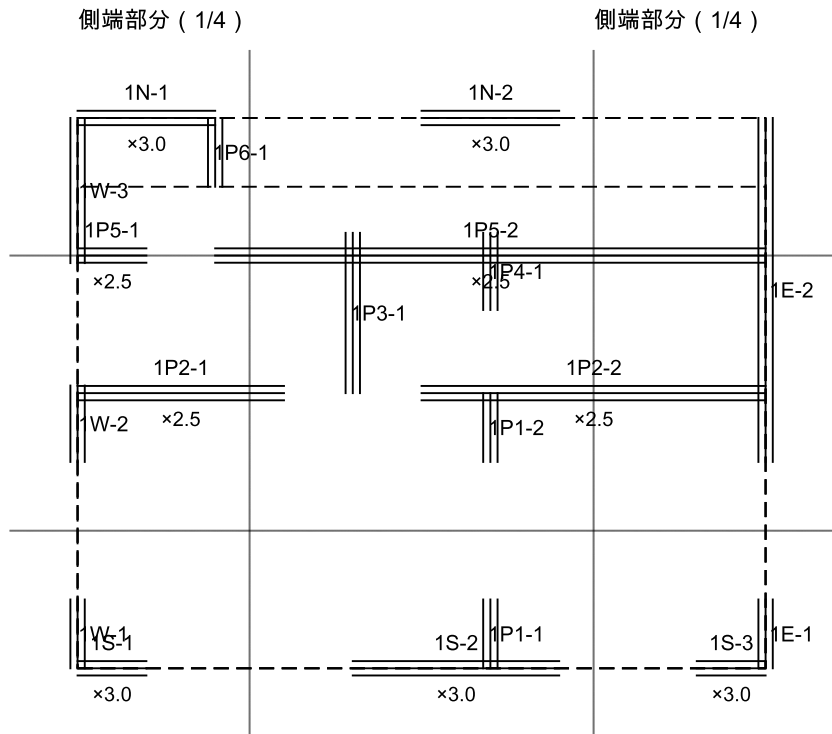

1階 耐力壁配置図 S=1:100

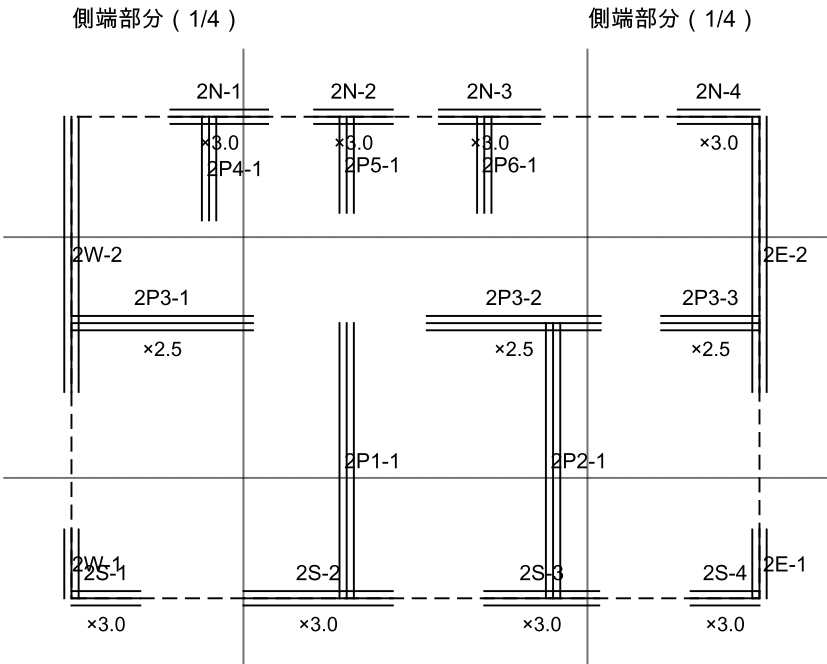

2階 耐力壁配置図 S=1:100

■ 存在壁量 (耐力壁一覧から機械で集計した値)

階	方 向	存在壁量 Σ(倍率×長さ) cm	床面積 m²	床面積あたり cm/m²
1階	X (東西)	6,324.5	66.25	95.47
1階	Y (南北)	4,257.5	66.25	64.27
2階	X (東西)	4,519.5	57.97	77.97
2階	Y (南北)	5,527.5	57.97	95.36

※ 必要壁量との比較・充足率・偏心率の判定は 03_計算書「構造計算書」に記載。この表は存在壁量の集計のみを示す。

【耐力壁の仕様】
外壁耐力壁 壁倍率 3.0
構造用合板 t9 片面張り / CN50 @100 (外周部)
内部耐力壁 壁倍率 2.5
構造用合板 t9 片面張り / CN50 @150
たて枠 2×6 (38×140) @455 上枠・下枠 2×6
頭つなぎ 2×6 (継手は 1,200 以上ずらす)

【壁倍率の根拠】
枠組壁工法の耐力壁の倍率は 平成13年国土交通省告示 第1541号による。上記は設計者指定値であり、実施設計では採用する面材・くぎの仕様を確定したうえで再確認すること。

【四分割法】
各方向について建物を4分割し、両端 1/4 (側端部分) の壁量充足率を確かめる。判定は 03_計算書に記載。

【共通注記】
1. 寸法の単位は mm。特記なき限り通り芯 (壁芯) 寸法とする。
2. 構造は木造2階建 枠組壁工法 (2×6) とし、親会社 株式会社 新昭和「ウィザースホーム」の標準工法 (モノコック構造) に準拠する。
3. 本図面集は参考プラン (架空案件) である。実在の敷地・施主ではない。実施設計にあたっては敷地条件・地盤調査結果・各種申請の指導事項を反映すること。
4. 法適合の検算結果は 03_計算書「法令適合検算書」を参照。同書で『未検算』とした項目は合格ではない。

内部耐力壁：壁倍率 2.5
外壁耐力壁：壁倍率 3.0

耐力壁配置図 (1階・ 2階)	
設計者	株式会社 Design RAVO
発注者	株式会社 新昭和 (親会社)
作成日	2026-09-14
縮 尺	S=1:100
図面番号	S-04