


立面図 (南・ 東・ 北・ 西) S=1:100

新昭和グループ 標準仕様 2×6 戸建住宅 参考設計図書
WITH EARTH / ウィザースホーム仕様 木造2階建 新築工事

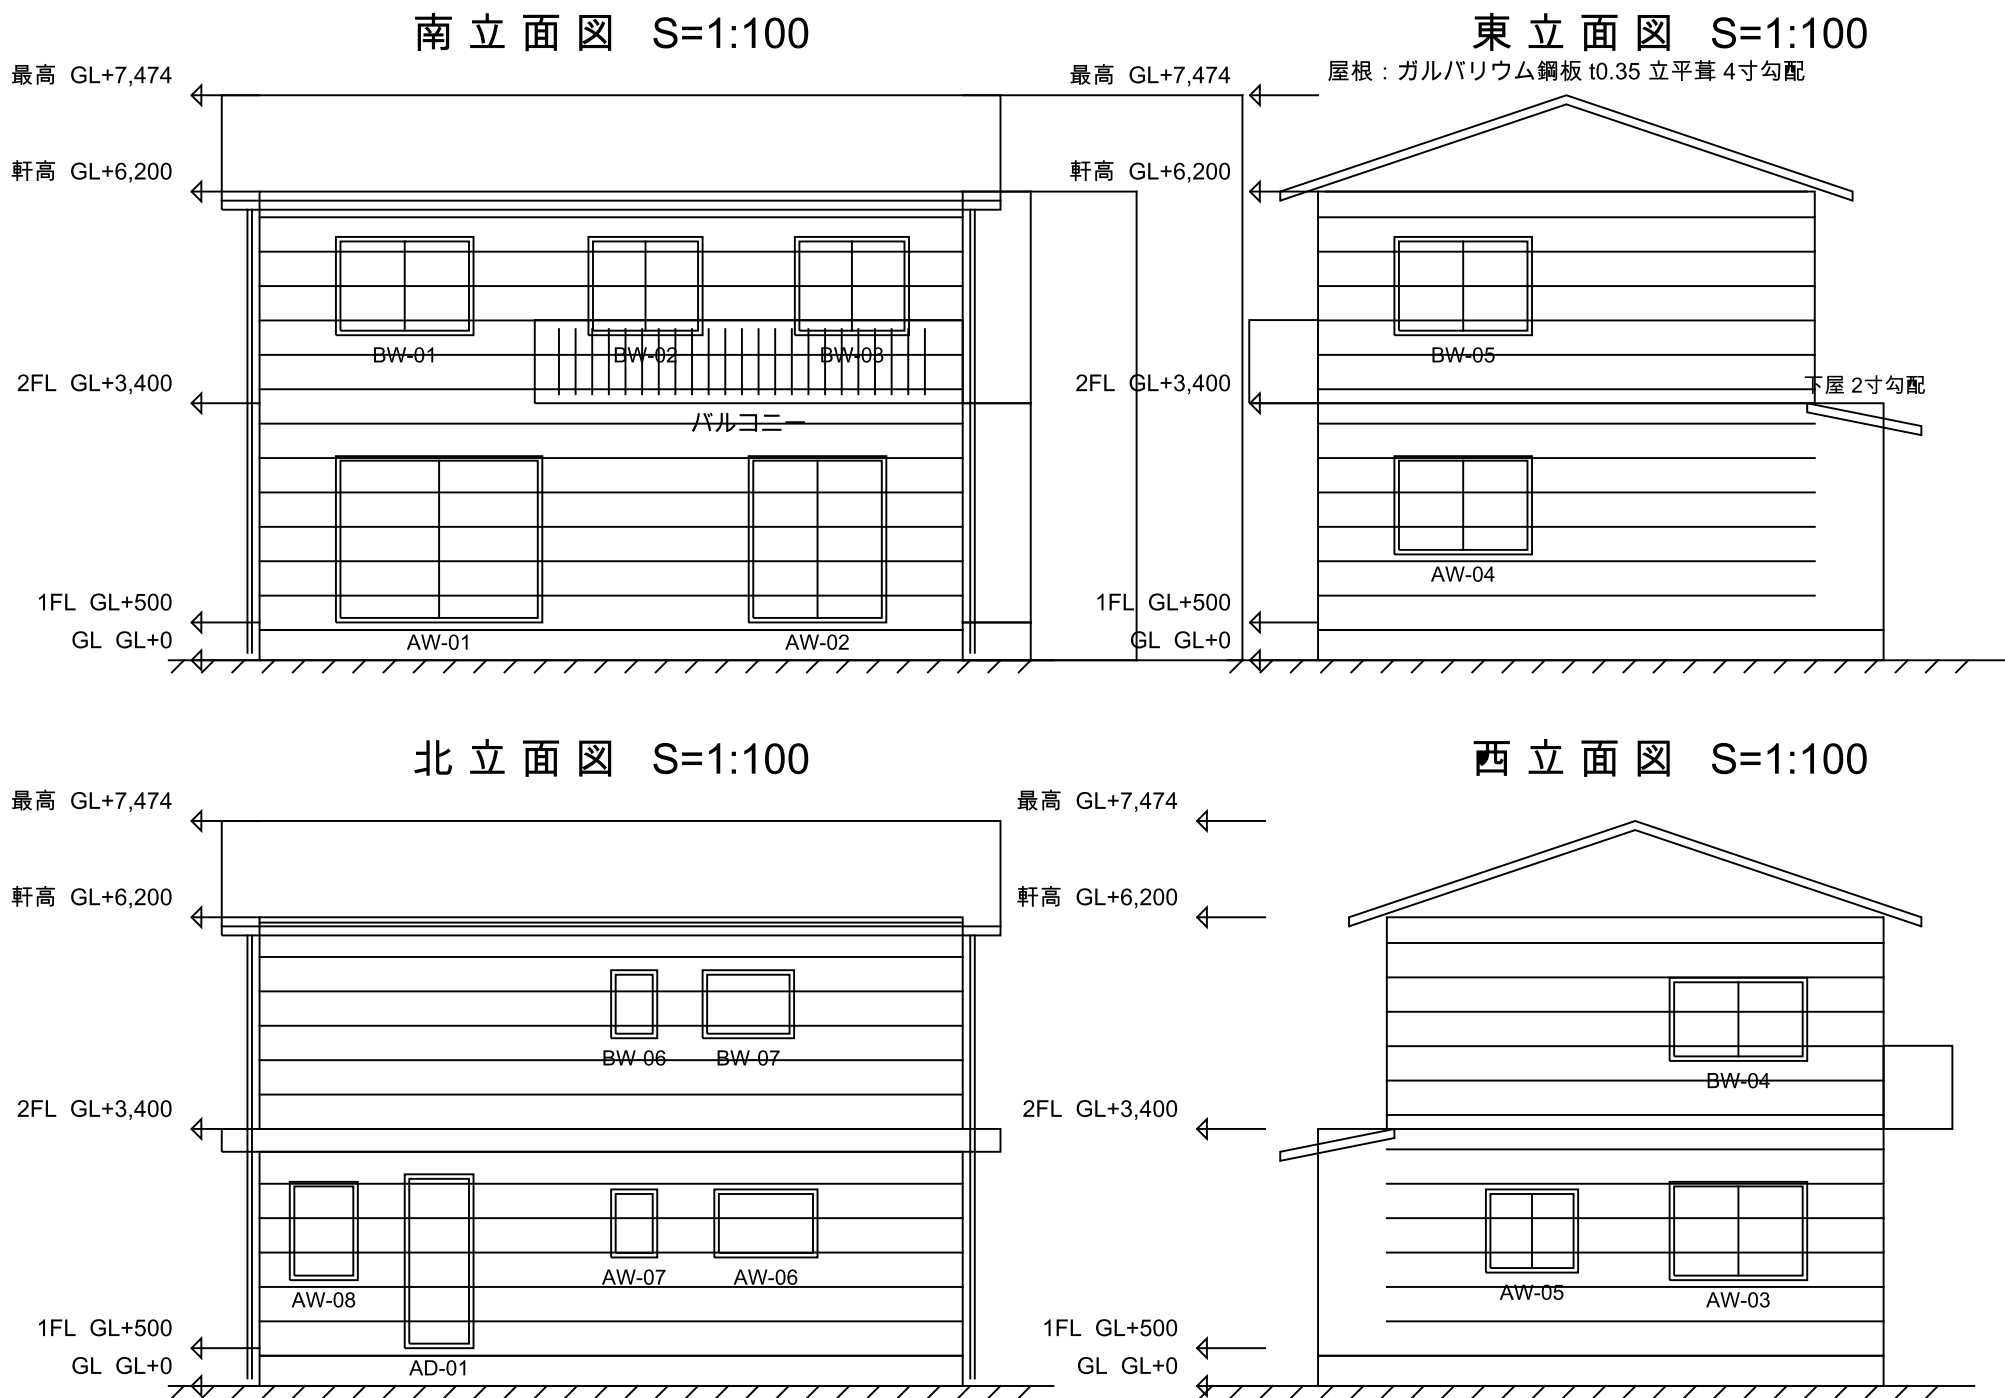

【外部仕上げ】
屋根：ガルバリウム鋼板 t0.35 立平葺 (主屋根 4寸勾配)
下屋は2寸勾配とする
外壁：乾式外装タイル 45二丁 / 通気胴縁 t18
透湿防水シート / 構造用合板 t9
軒裏：けい酸カルシウム板 t6 準不燃・軒天換気材
とい：たてとい φ60 / 軒どい 半丸105
建具：樹脂サッシ + Low-E複層ガラス (アルゴン入)

【高さ関係】
最高の高さ GL+7,474
軒の高さ GL+6,200
1階階高 2,900 / 2階階高 2,800
天井高 2,400 (浴室を除く)

【見方】
北立面は北から見た姿 (図の右が西)。
西立面は西から見た姿 (図の右が南)。
2階を南へ 910 後退させ、1階の張出し部に下屋を架けている。

【共通注記】
1. 寸法の単位は mm。特記なき限り通り芯 (壁芯) 寸法とする。
2. 構造は木造2階建 枠組壁工法 (2×6) とし、親会社 株式会社
新昭和「ウィザースホーム」の標準工法 (モノコック構造) に
準拠する。
3. 本図面集は参考プラン (架空案件) である。実在の敷地・施主
ではない。実施設計にあたっては敷地条件・地盤調査結果・
各種申請の指導事項を反映すること。
4. 法適合の検算結果は 03_計算書「法令適合検算書」を参照。
同書で『未検算』とした項目は合格ではない。

軒の高さ：GL+6,200
最高の高さ：GL+7,474

立面図 (南・ 東・ 北・ 西)	
設計者	株式会社 Design RAVO
発注者	株式会社 新昭和 (親会社)
作成日	2026-09-14
縮 尺	S=1:100
図面番号	A-05