


小屋伏図 S=1:50

新昭和グループ 標準仕様 2×6 戸建住宅 参考設計図書
WITH EARTH / ウィザースホーム仕様 木造2階建 新築工事

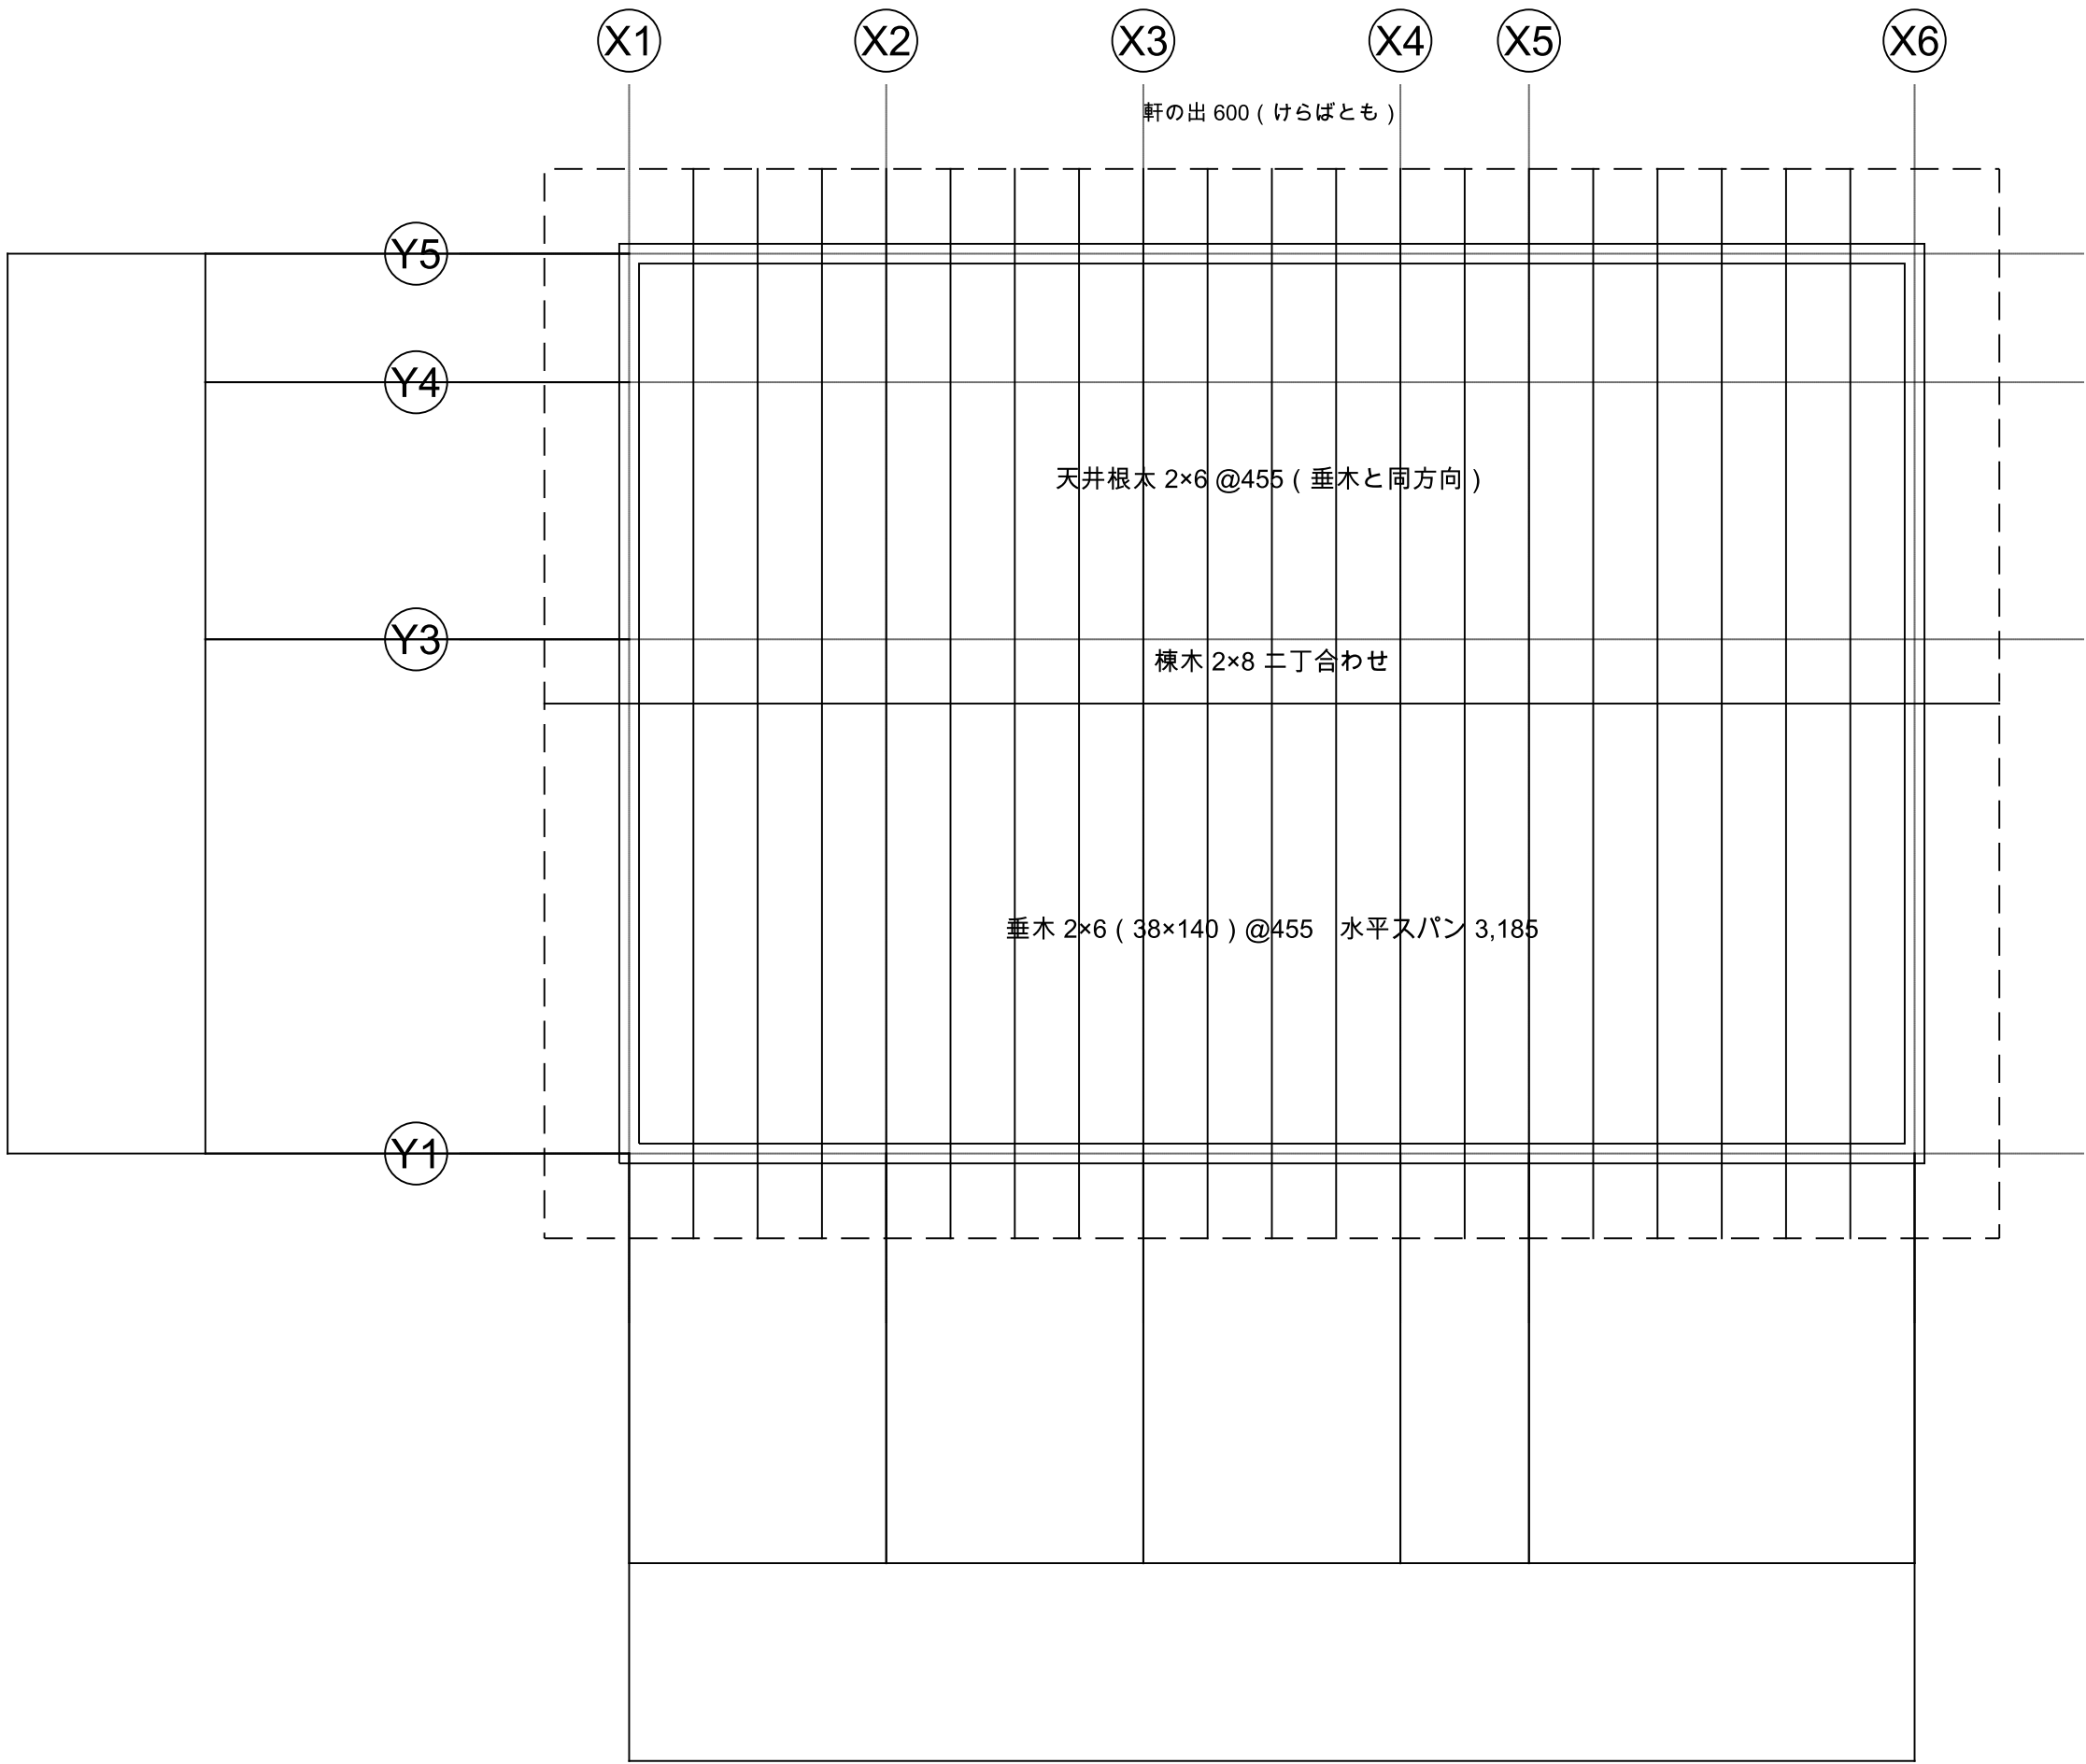

【小屋組】
垂木 2×6 (38×140) @455 水平スパン 3,185
棟木 2×8 二丁合わせ
天井根太 2×6 (38×140) @455
構造用合板 t12 (野地) / 改質アスファルトルーフィング
あおり止め金物を垂木・軒桁の取合いに全数設ける。

【小屋裏】
吹込みグラスウール 18K t300
軒天換気材により小屋裏換気を確保する。

【積雪・風について】
積雪時・暴風時の検定は、垂直積雪量 (特定行政庁が定める) と基準風速 (告示第1454号) が確定してから行います。これらは所在地で決まる値のため、当方で数値を作ることはしていません。03_計算書では『未検算』として開示しています。

【共通注記】
1. 寸法の単位は mm。特記なき限り通り芯 (壁芯) 寸法とする。
2. 構造は木造2階建 枠組壁工法 (2×6) とし、親会社 株式会社 新昭和「ウィザースホーム」の標準工法 (モノコック構造) に準拠する。
3. 本図面集は参考プラン (架空案件) である。実在の敷地・施主ではない。実施設計にあたっては敷地条件・地盤調査結果・各種申請の指導事項を反映すること。
4. 法適合の検算結果は 03_計算書「法令適合検算書」を参照。同書で『未検算』とした項目は合格ではない。

小 屋 伏 図 S=1:50

屋根勾配 : 4寸
垂木 : 2×6 (38×140) @455

小屋伏図	
設計者	株式会社 Design RAVO
発注者	株式会社 新昭和 (親会社)
作成日	2026-09-14
縮 尺	S=1:50
図面番号	S-03